

京张·复面

公园成园之后，城市再次面向京张。

一园双面，三类创新前沿

以真实横路与公共节点为接棒条件的非对称复面

—— 科研复面

—— 校城复面

—— 站城复面

证据边界：概念设计可推进；工程实施待门、柱网、权属、消防与后勤条件的专业核验。



先读图，再读边界

24 页把空间主张、证据上限与专业深化条件放在同一条阅读线上。

01 总体结构

证据边界 / 三层范围 / 复面长卷 / 非对称机制

02 重点片区

众智园 / AI 原点 / 大钟寺 / 三类前沿

03 AI 原点

两锚一接点 / 总平 / 首层 / IF-01 / IF-02 / S2

04 场景与人物

十张场景卡 / 四个英雄场景 / 七类人物

05 实施与复核

分期触发 / 运营治理 / 非退化台账 / 专业解锁

四种线，四种证据状态

现状 / 已核线索

概念主复面

保底复面

待核接点 / 变量尺寸

读图顺序

- 1 先看空间动作
- 2 再看证据条
- 3 最后看解锁条件

图纸是解释层；GeoJSON、metrics 与矩阵是复核层。

概念可以前进，工程仍然锁定

同一张图同时说清楚：知道什么、假设什么、设计什么，以及下一步由谁核验。

知道 / KNOW	赛事公告、任务书、公开资料与冻结 OSM 只在其许可范围内支撑判断。
假设 / ASSUME	临时 polygon、未测入口、柱网、停车、消防、权属与工程边界保持虚线。
设计 / DESIGN	M 方案可以提出参数化首层前沿带、院前阈值、静态导视和可撤运营。
核验 / VERIFY	产权、结构、消防、交通、医疗、无障碍、生态、市政与运营主体逐项解锁。

```
concept_design_eligible=true / engineering_implementation_verified=false / M_CONCEPT_DESIGN=GO / M_ENGINEERING_IMPLEMENTATION=LOCKED
```

三层范围，不混成一张红线

统筹研究、总体设计与重点区域分别承担战略、空间组织和类型验证。

01

统筹研究范围

43.6 km²

为什么更新

产业与未来城市判断；不产生地块控制。

02

总体设计范围

11.4 km²

沿线如何组织

复面长卷、双侧界面与交通蓝绿；不报精确双侧长度。

03

重点区域范围

368.4 ha

空间如何工作

三类前沿、AI 原点样段、平面、剖面、场景与分期。

43.6 km²、11.4 km² 与三处共 368.4 ha 均为公告文字参考规模。当前 polygon 是临时约束，不是官方红线，也不用于精确面积、权属或工程判断。



复面长卷：既有公共脊与双侧城市界面的第二次更新。

01 / SPATIAL SIGNATURE

一园双面，三区两翼

ONE PARK, TWO FRONTS, THREE ZONES + TWO WINGS

复面不是再造一条景观轴，而是让公园两侧的首层、院前与后勤系统重新建立公共关系。

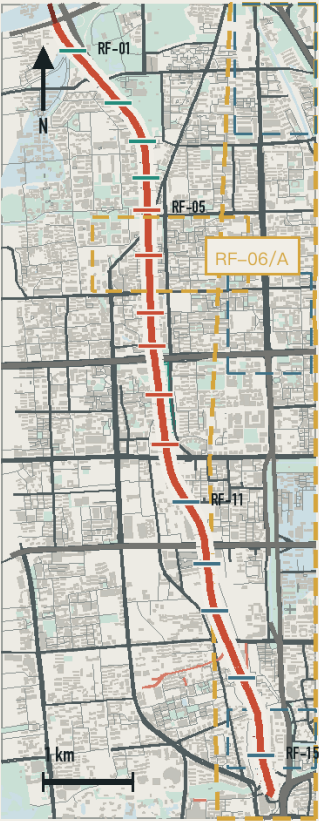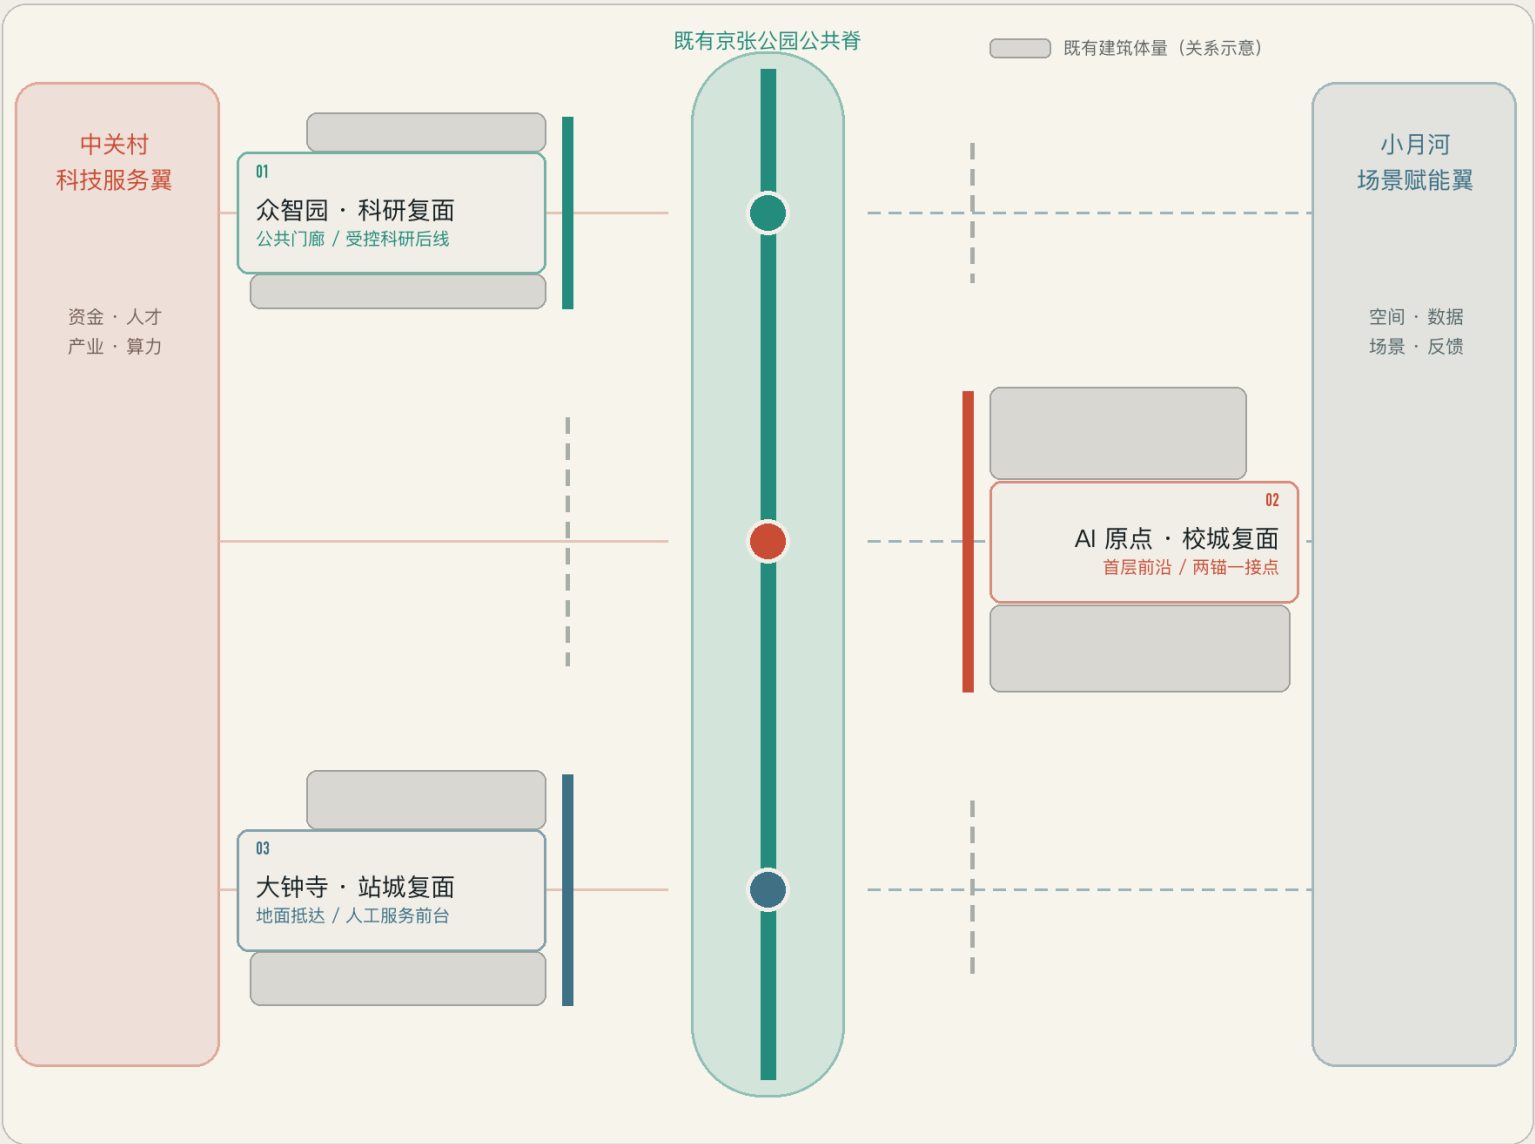

证据底图 / 冻结 OSM
十五段是分析带；两翼是服务关系。均不等同于法定边界、道路或已批准工程。

主复面：有真实公共节点才加深

保底复面：维持通行、生态与运维

接棒：合法落点成立才换侧

DESIGN SIGNATURE + OSM TYPE 1:18,000 · NORTH UP
概念设计可推进 / 工程实施待专业核验

OSM © CONTRIBUTORS, ODbL 1.0 · SNAPSHOT 2026-08-28T14:20:06Z
空间母图为概念关系；OSM 研究框架≠法定红线

把首层转向公园


一园双面：主复面、保底复面与首层前沿带。

02 / ECOSYSTEM MAP

三区两翼 × 八要素

THREE ZONES + TWO WINGS × EIGHT ENABLERS

把产业生态翻译成空间载体、人工责任与可停止的项目机制；连线表示服务关系，不表示道路、管线或产权。

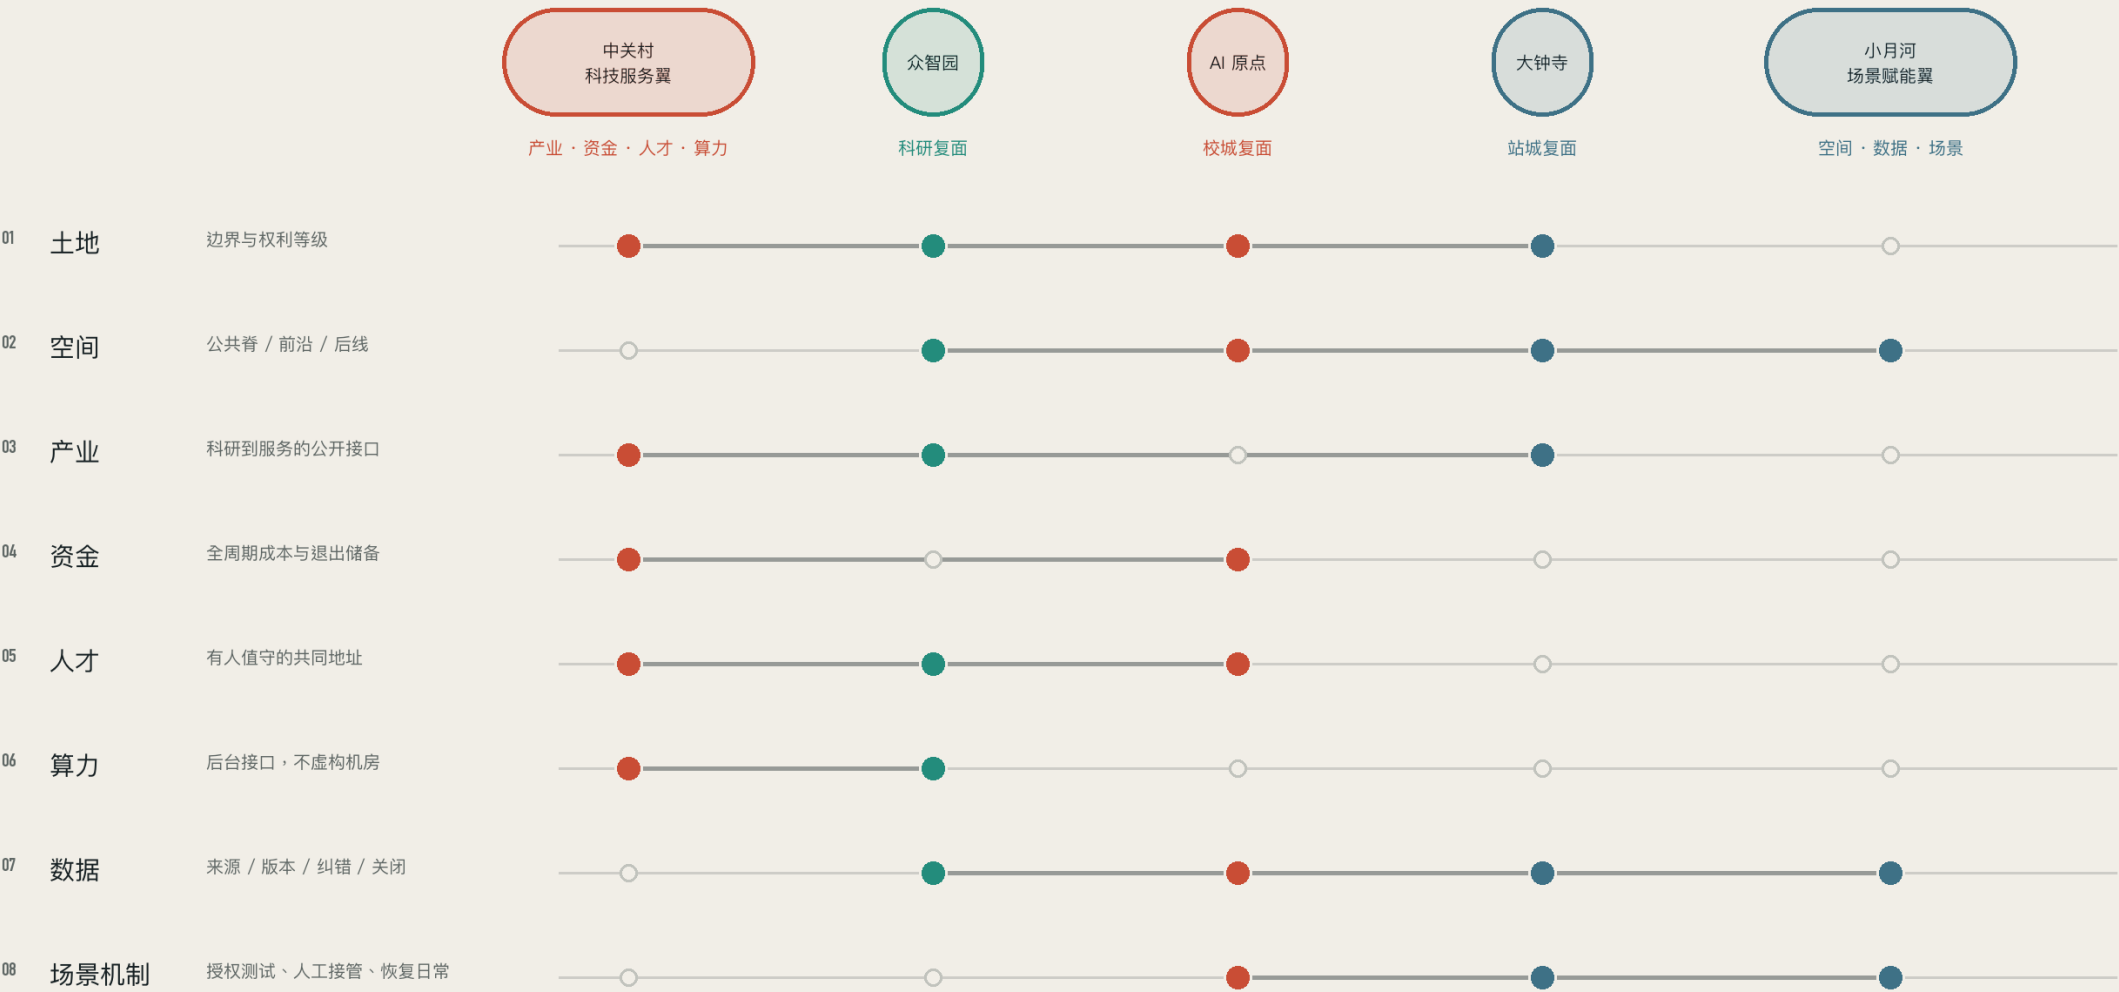

十个项目包

P01 EVIDENCE

P06 ARRIVAL

P02 RESEARCH

P07 LANDMARKS

P03 IF-01

P08 AI-OFF

P04 IF-02

P09 TVS

P05 S2

P10 OPERATIONS

ECOSYSTEM RELATIONSHIP MAP / NOT TO SCALE

概念设计可推进 / 工程实施待专业核验

OSM © CONTRIBUTORS, ODbL 1.0 · SNAPSHOT 2026-08-28T14:20:06Z

实线=主承载；空心点=协同或待核。所有关系须由权利主体与运营责任解锁。


真实横路、合法过街、公共节点与后勤连续线共同决定接棒。

04 / PUBLIC GROUND SYSTEM

公园是一条公共地面，不是一条展示带

THE PARK IS CIVIC GROUND, NOT A DISPLAY STRIP

普通通行、无障碍、蓝绿基线与后勤连续先成立；复面与 AI 只能进入剩余且可恢复的空间。

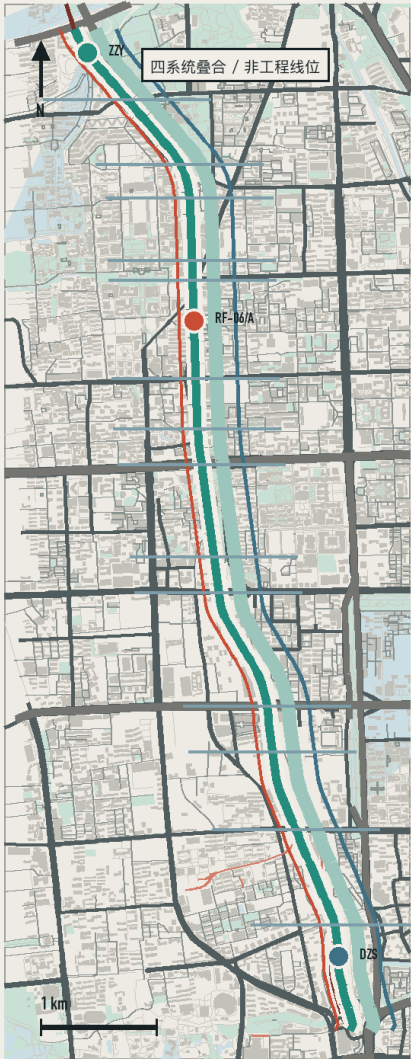


四条不可被展示挤占的线

- 01 普通通行
净宽 · 开放时段 · 设计能力 ≥ 基线
- 02 无障碍与人工帮助
逐段核路；静态与人工路径始终存在
- 03 蓝绿与日常维护
零移树建议；树冠、渗透、雨洪与养护不退
- 04 消防、装卸、清运与检修
全部已核必要端点保持 100% 可达

S2 / 双清路：一个接棒测试

东向合法落点未证

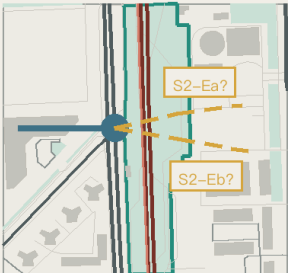

合法落点 + 连续无障碍 + 普通通行 + 权属/消防全部通过，才允许换侧。

CORRIDOR TYPE 1:18,000 + S2 INSET TYPE 1:4,000 · NORTH UP

概念设计可推进 / 工程实施待专业核验

OSM © CONTRIBUTORS, ODbL 1.0 · SNAPSHOT 2026-08-28T14:20:06Z

四条线为概念系统语法；S2 东向落点为条件虚线，未宣称新增贯通

S2 东向合法落点未证实：只画测试，不计算新增贯通。

同一公共脊，三种前沿

科研复面、校城复面、站城复面采用同一尺度比较，但不复制同一形式。


03 / THREE FRONTS

三种冲突，三种复面

THREE CONFLICTS, THREE RE:FRONT TYPES

同一比例尺下，把问题、空间动作、人工终决与停止条件放在同一张图上。

01 众智园
科研复面

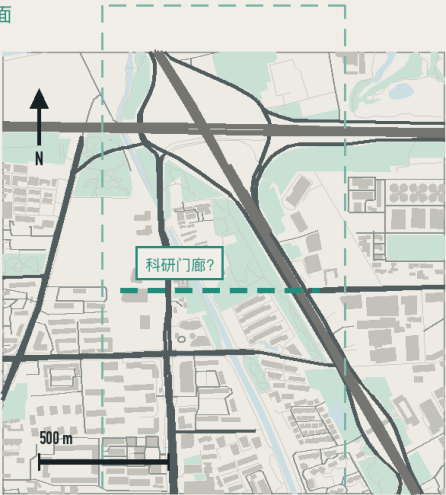

- 冲突

公众希望看见科研，但实验安全、知识产权与运维后线不能被穿透。
- 空间动作


把经核入口组织为公共门廊；公众停在可观察前场，研发与检修走独立后线。
- 组件 / 终决

科研门廊 + 人工答疑 + 开源刻度；科研/IP/运营人员终决。
- 停止条件

入口、版权或前后场分离未证；妨碍普通通行；无人值守。

边界、入口与科研前后场均待官方/现场核验。

02 AI 原点
校城复面

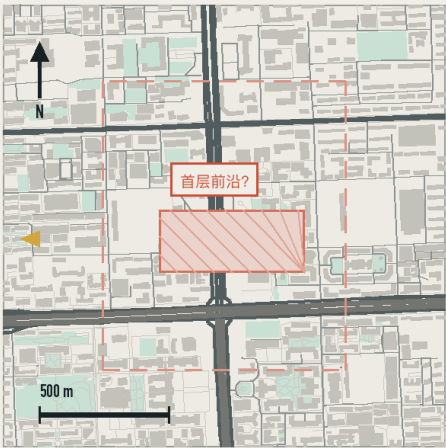

- 冲突

创新活动、门诊、社区服务、停车落客、消防与后勤争用同一条沿园界面。
- 空间动作

IF-01 前场共存，IF-02 保持有人服务；S2 只在合法东向落点成立后接棒。
- 组件 / 终决

两锚一接点 + 首层前沿带 + 复面档案架；运营、医疗、消防与社区人员终决。
- 停止条件

首层不能合法开放；停车/消防冲突未解；服务只能由 AI 完成；S2=NO-LINK。

PROV-KEY-002 与真实 A/Rf-06 空间错位；不静默平移。

03 大钟寺
站城复面



- 冲突

站口到达、换乘、无障碍、社区服务与日常通勤需要共享清晰地面。
- 空间动作

以静态到达语法连接经核站口、人工帮助、停留点与首层服务，不虚构综合交通工程。
- 组件 / 终决

地面抵达系统 + 抵达刻度 + 非数字组件；交通、无障碍、文化与运营人员终决。
- 停止条件

真实出入口或路线未核；静态替代缺失；干扰疏散、公交、落客或普通通行。

PROV-KEY-003 与真实站点错位；正式边界到位后重绑。

COMMON WINDOW = 1.7 km × 1.7 km · TYPE 1:10,000 · NORTH UP

概念设计可推进 / 工程实施待专业核验

OSM © CONTRIBUTORS, ODbL 1.0 · SNAPSHOT 2026-08-28T14:20:06Z

淡色虚线=仓库 provisional 约束；空间动作均为参数化概念建议

三处临时 polygon 均非官方红线。大钟寺临时重点区与真实锚点约 1.7 km（按临时几何计算）。

让科研可见，但不越界

众智园：公共观察、人工答疑与受控科研后线并存。



- 公共入口与共享首层经核实后形成共同公共地址。
- 经审样品、研究目录与人工答疑构成可旁观门廊。
- 受控实验、样品运送、设备检修与科研安全线保持独立。
- 桥下或河边硬地等待防洪、桥梁、消防与运维复核。

两锚一接点：AI 原点复面样段

IF-01、IF-02 与 S2 共同验证首层、院前、公园和后勤能否共存。


06 / AI ORIGIN MASTERPLAN

两锚一接点：AI 原点复面样段

TWO ANCHORS, ONE TEST: AI ORIGIN RE:FRONT DEMONSTRATOR

以 IF-01、IF-02 和 S2 验证首层、院前、公园普通通行与后勤能否共存。

主复面
EAST CANDIDATE

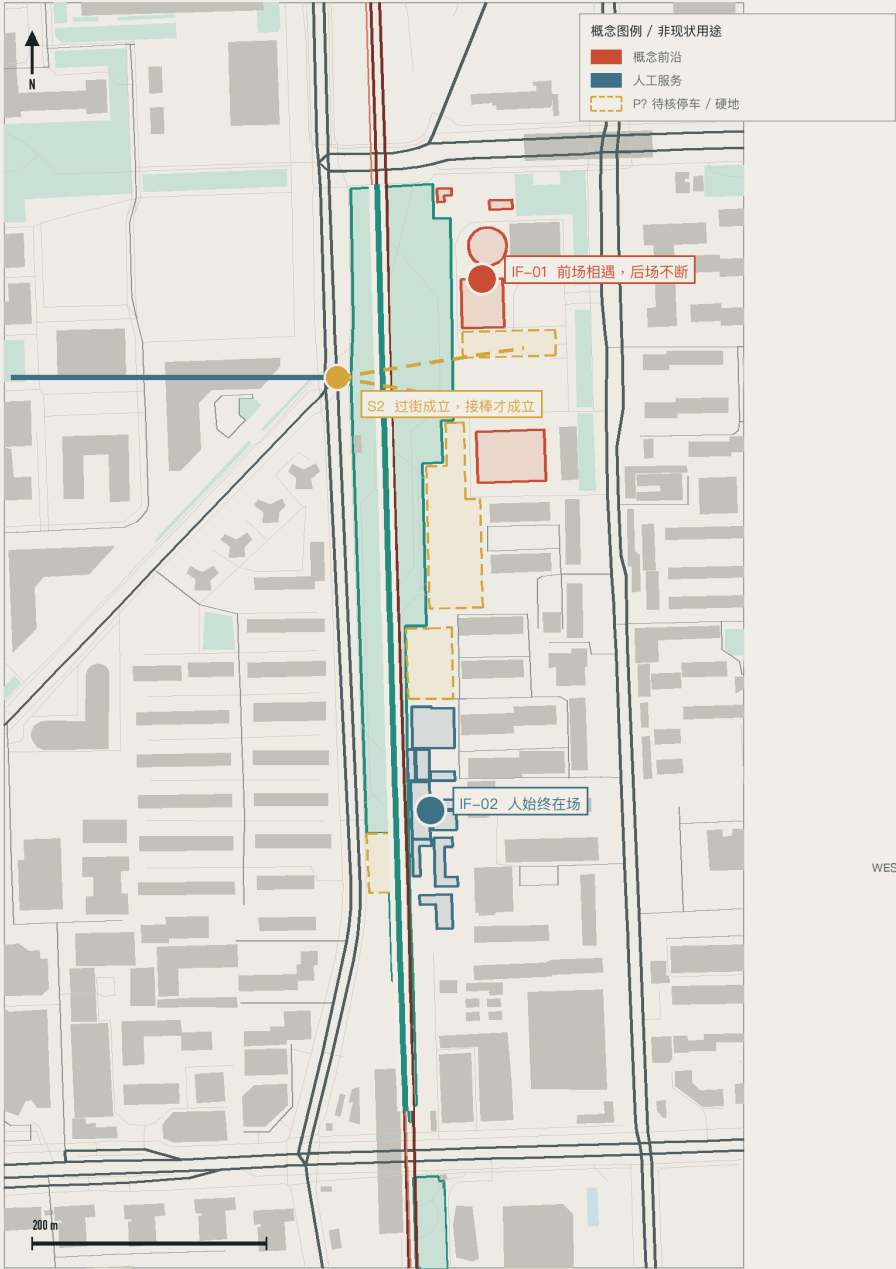

保底复面
WEST / NO FORCED SWITCH

双框架披露	
框架错位	真实 OSM A/RF-06 与仓库 PROV-KEY-002 不相交，最小约 580 m。本图仅使用真实 OSM 研究框架。
工程锁定	门、柱网、停车性质、产权、消防、落客、后勤与工程边界。



- IF-01：创新活动、门诊、停车、落客、消防与后勤并存；就诊和安全始终优先。
- IF-02：公共服务与人工治理锚点；不做 AI 展厅。
- S2：西侧横路线索可见；东向合法落点未证，不宣称新增贯通。
- 真实研究窗口 RF-06/A 与临时 PROV-KEY-002 错位，图上并置披露。

首层前沿带—后勤换位

约一个结构开间只是参数上限；门、柱网、消防、停车与权属未核前保持虚线和备选状态。


07 / GROUND-FLOOR INTERFACE

首层前沿带—后勤换位

GROUND-FLOOR INTERFACE STRATEGY: PUBLIC THRESHOLD AND LOGISTICS REPOSITIONING


建筑轮廓来自冻结 OSM；内部不绘制未证实的房间、柱网和门，前沿深度仅为变量。

IF-01 前场相遇，后场不断

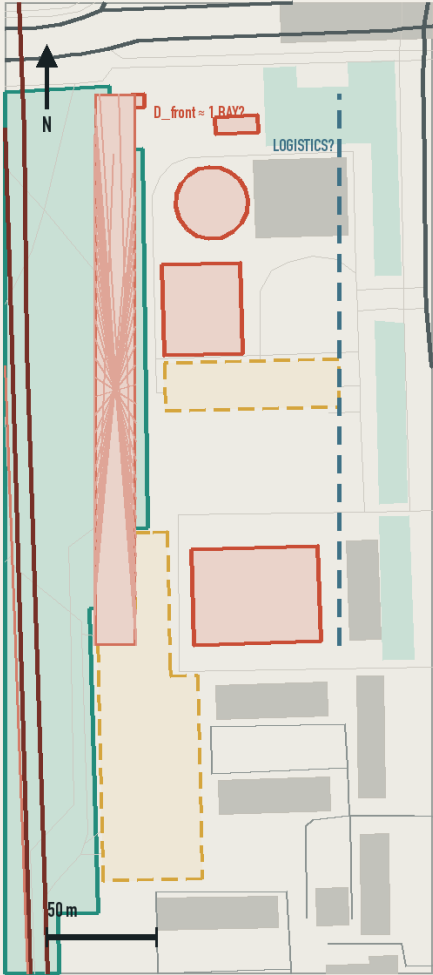

D 座一层已有创新活动与门诊线索；B/C 为 OSM 映射。C 座存在同名 footprint 冲突，标 C? 待核。P? 只在停车替代、落客、消防和排水通过后释放。

IF-02 人始终在场

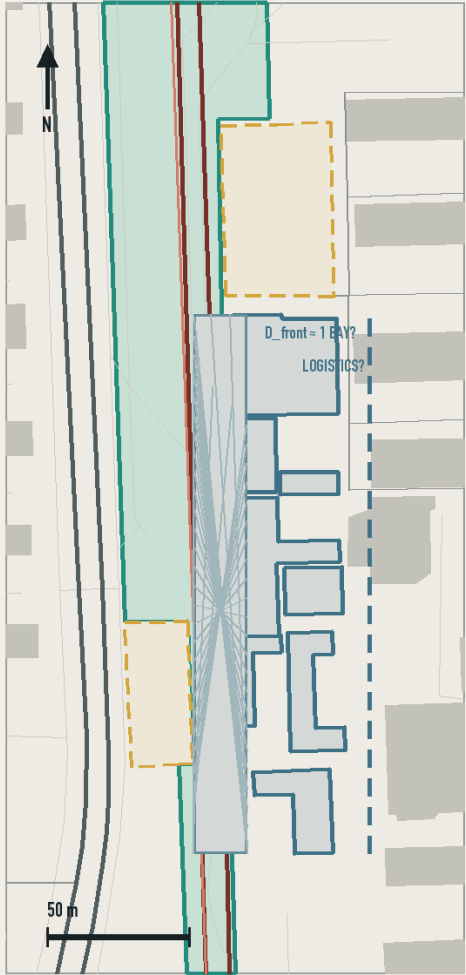

27 号院是公共服务与人工治理锚点，不做 AI 展厅。卫生站具体楼栋、临园门、医疗废物/急救、住宅门禁与消防均待核。

TWO TYPE WINDOWS ≈ 1:500 CONCEPT RELATION · NORTH UP · 50 m BAR

概念设计可推进 / 工程实施待专业核验

OSM © CONTRIBUTORS, ODbL 1.0 · SNAPSHOT 2026-08-28T14:20:06Z

斜线 = 首层前沿带候选；P? = 停车/硬地待核；蓝虚线 = 后勤原则路径

前场相遇，后场不断

创新活动与门诊共享前沿带；落客、消防和后勤保持连续。

08 / IF-01 TYPE SECTION

前场相遇，后场不断

MEET AT THE FRONT, KEEP THE BACK RUNNING

创新活动、门诊、落客、消防与后勤共享同一首层界面，但不共享必要安全线。

EXISTING / 现状


映射建筑轮廓 / 首层与净宽未核

L / 0-1 YEAR

可撤导视 + 人工台 + 纸面时表

M / CONCEPT 60

条件式首层前沿 + 院前公共阈

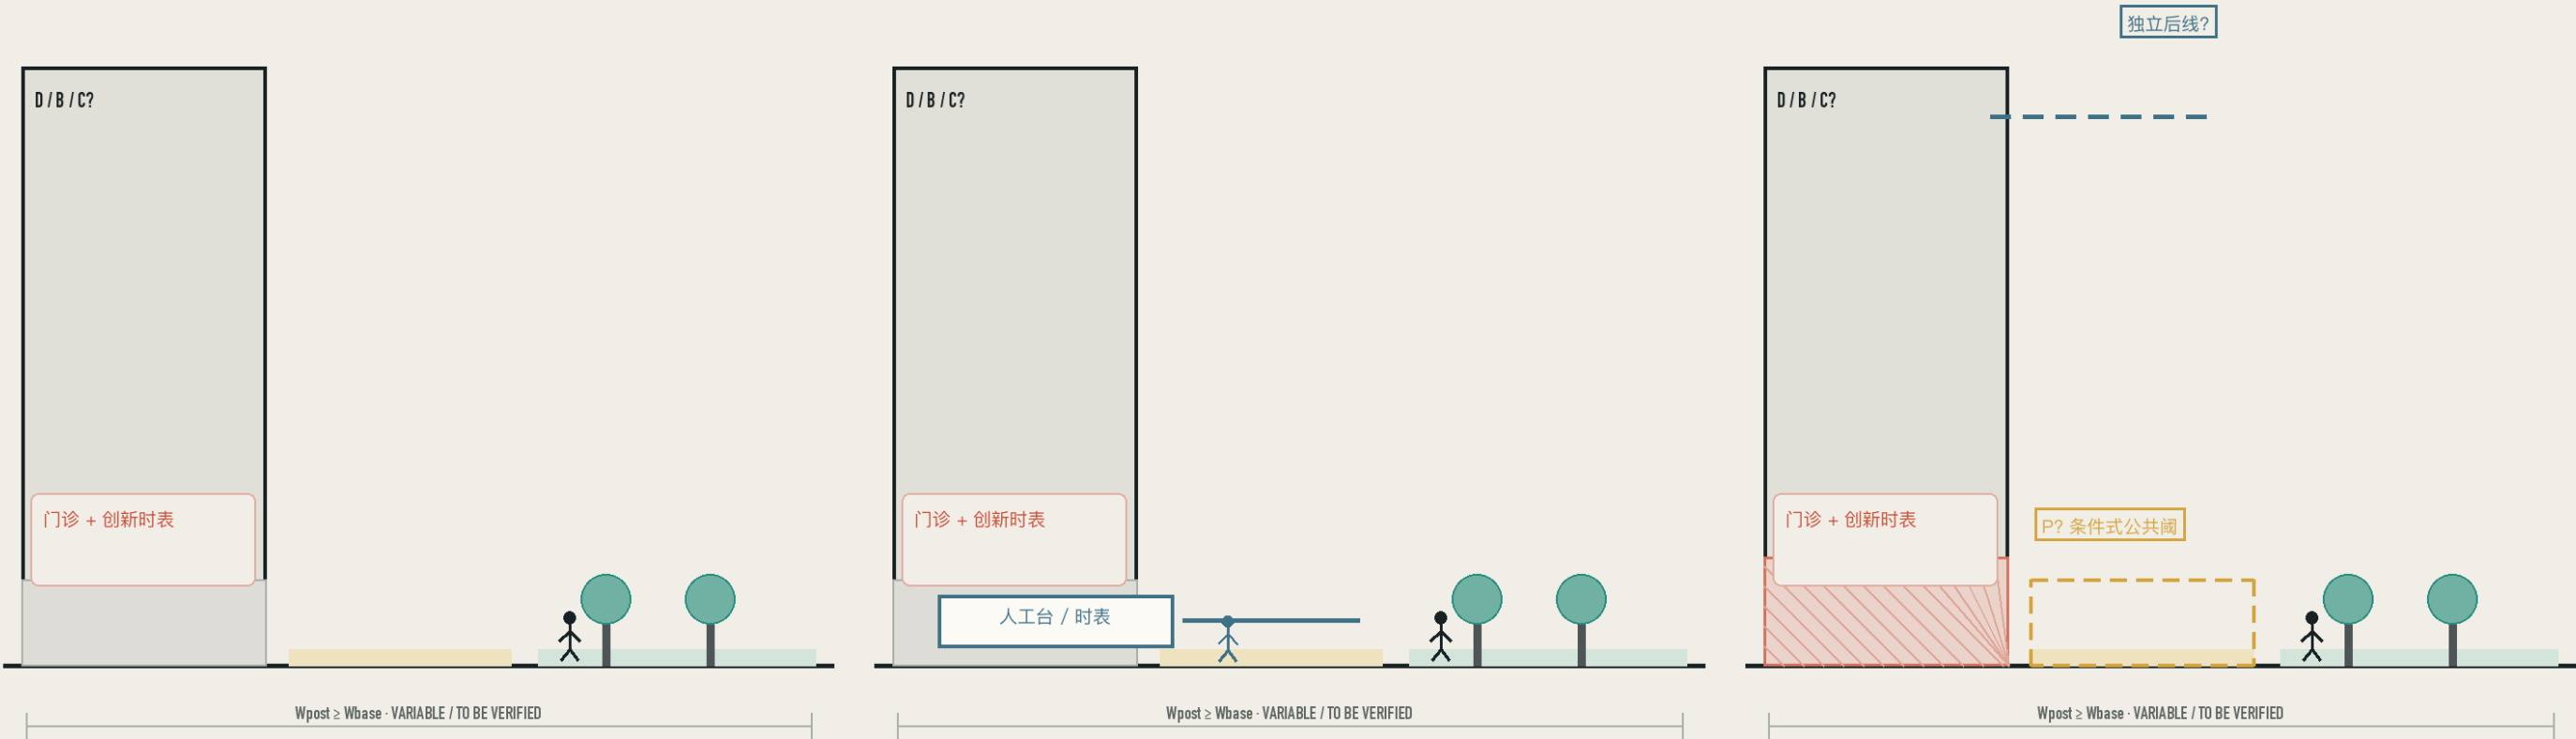

TYPE SECTION ≈ 1:500 CONCEPT RELATION · HORIZONTAL REFERENCE ONLY · NORTH N/A

概念设计可推进 / 工程实施待专业核验

OSM © CONTRIBUTORS, ODbL 1.0 · SNAPSHOT 2026-08-28T14:20:06Z

门、柱网、门诊急救、消防登高、停车与装卸待核；C? 为 OSM 同名冲突

人始终在场

公共服务与人工治理锚点，不设置 AI 展厅。

09 / IF-02 TYPE SECTION

人始终在场

PEOPLE REMAIN PRESENT

公共服务与人工治理先于 AI 展示；拒绝 AI 不影响办事与医疗服务。

EXISTING / 现状


映射建筑轮廓 / 首层与净宽未核

L / 0–1 YEAR

可撤导视 + 人工台 + 纸面时表

M / CONCEPT 60

条件式首层前沿 + 院前公共阈

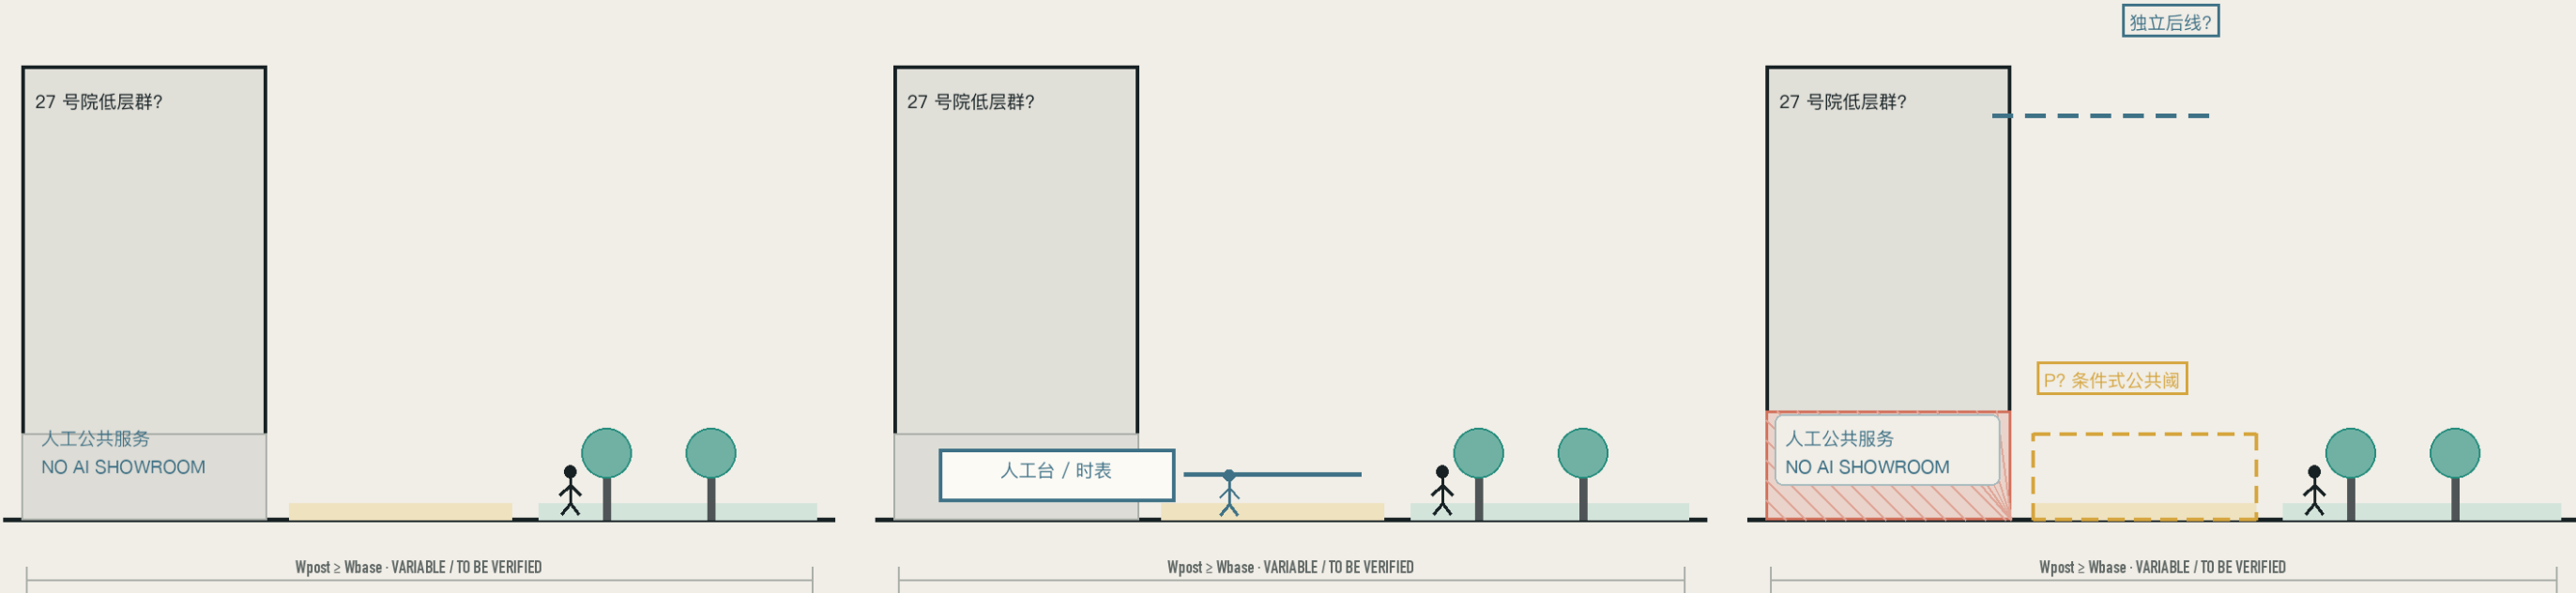

TYPE SECTION ≈ 1:500 CONCEPT RELATION · HORIZONTAL REFERENCE ONLY · NORTH N/A

概念设计可推进 / 工程实施待专业核验

OSM © CONTRIBUTORS, ODbL 1.0 · SNAPSHOT 2026-08-28T14:20:06Z

具体楼栋/临园门、医疗废物/急救、住宅门禁与消防待核；不做 AI 展厅

过街成立，接棒才成立

东向合法落点未证实前，只表达横向连接测试。

10 / S2 TYPE SECTION

过街成立，接棒才成立

THE HANDOVER FOLLOWS A PROVEN CROSSING

只有合法东向落点、连续无障碍、普通通行与物业/消防共同通过，复面才换侧。

EXISTING / 现状


西侧真实横路 / 东向落点未证

L / 0–1 YEAR

现状过街信息 + 人工无障碍协助

M / CONCEPT 60

Ea / Eb 条件比选 / 不全则 NO–LINK

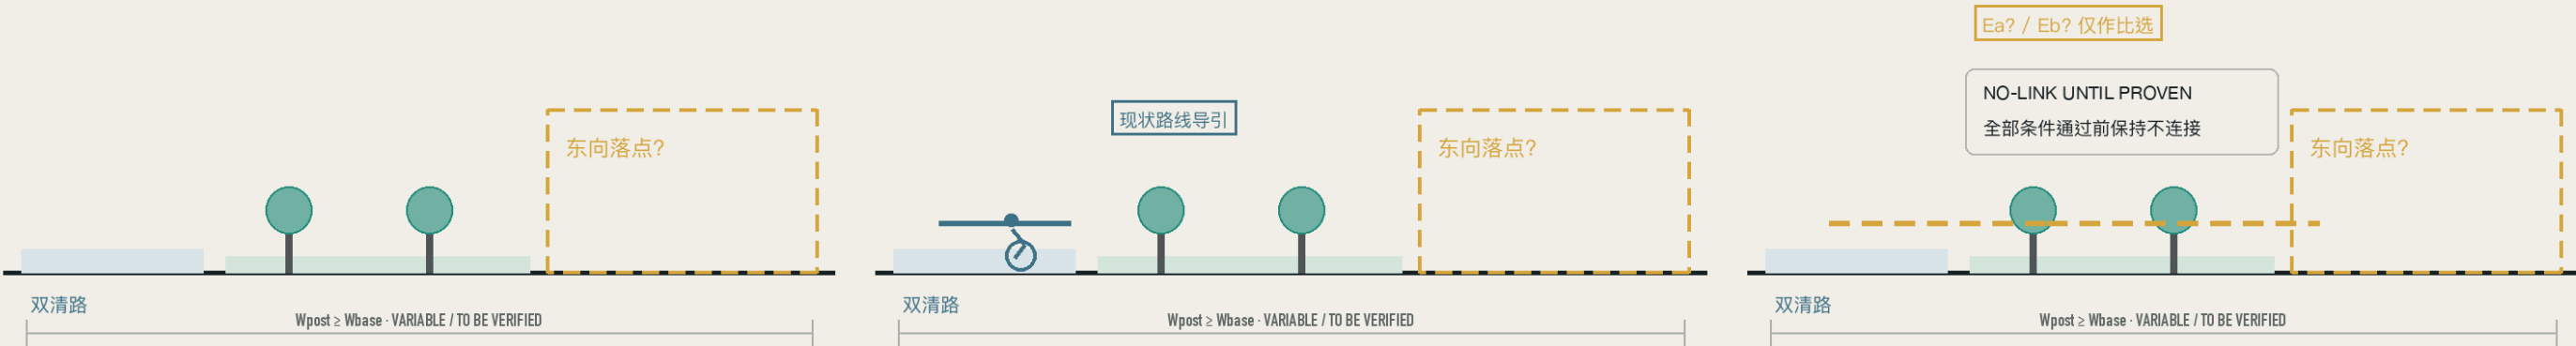

TYPE SECTION ≈ 1:500 CONCEPT RELATION · HORIZONTAL REFERENCE ONLY · NORTH N/A

概念设计可推进 / 工程实施待专业核验

OSM © CONTRIBUTORS, ODbL 1.0 · SNAPSHOT 2026-08-28T14:20:06Z

信号属性、净宽/流量、东向合法落点与物业/消防待核；不宣称新增贵通

让到达与服务在地面相遇

大钟寺：站口、换乘、社区服务与公园普通通行共享可读地面。

概念体验图 / 非现状、非批准



- 先把找出口、找公园、找无障碍路与找公共服务放进同一张地面到达图。
- 静态导视、触觉路径与人工服务构成 AI-off 基线。
- 站口疏散、公交/落客、消防、权属与无障碍均通过后，才讨论可撤公共阈值。
- 临时重点区与真实大钟寺锚点约 1.7 km（按临时几何计算）；需官方边界校正。

三种前沿，是三种空间关系

科研、校城与站城可以并行发生，不构成必须由北向南发生的产业链。

03B / OPTIONAL DIAGRAM

三种前沿的空间语法


THE SPATIAL GRAMMAR OF THREE FRONTS

这是可选机制图；正式核心图 key--areas.png 使用真实 OSM 底图与同尺度视窗。

01

让科研可见，但不越界


可控观察 / 安全边界 / 独立后线

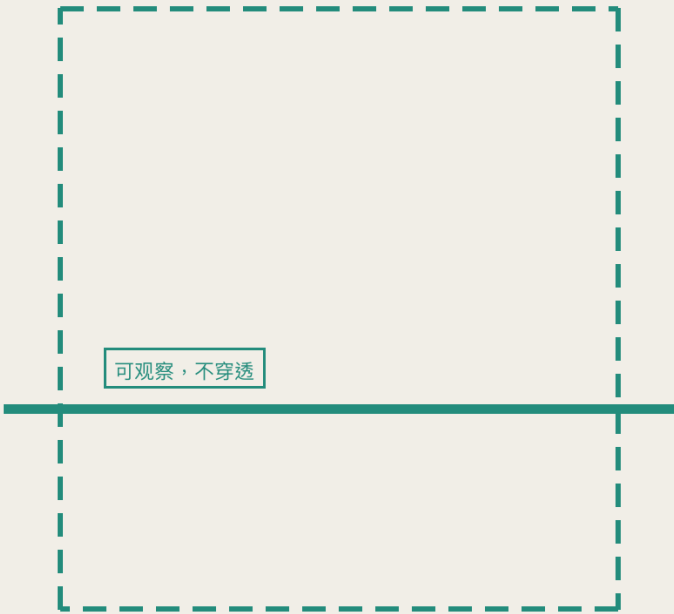

02

把首层变成创新前厅


首层前沿 / 院前阈值 / 人工服务

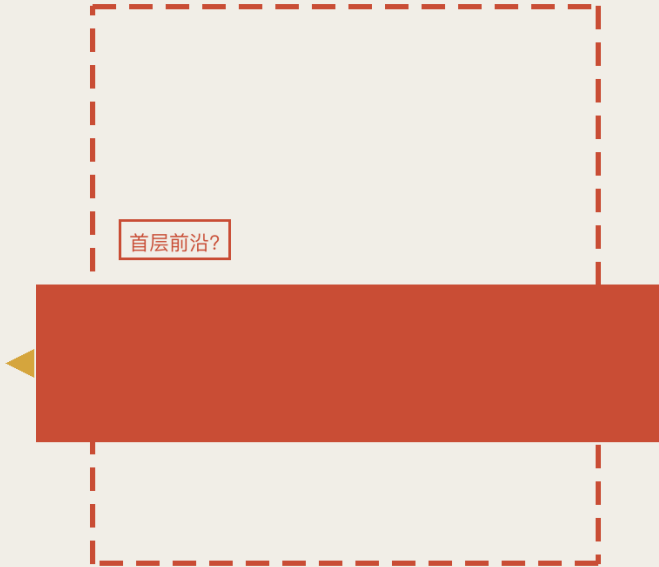

03

让到达与服务在地面相遇

站口到达 / 普通通行 / 平行后线

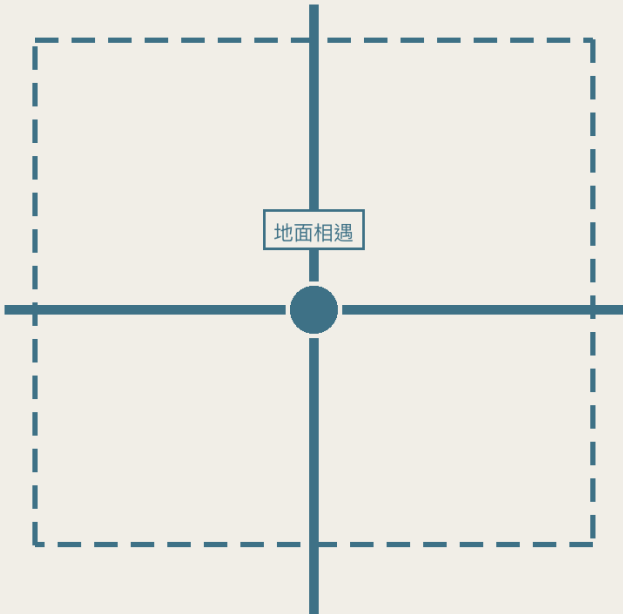

科研协作、跨运营时表、诊疗导引与公共服务都保留非数字入口。

SC-01

看得见的试验，不越界的科研

众智园公共门廊



只检索公开、已清权的项目与专家目录。

人工确认引荐；不读实验数据。关闭后保留纸质目录。

SC-02

诊疗、创新、检修，不在同一分钟抢一扇门

IF-01 / 跨运营时表 TVS



提示诊疗、活动、装卸与检修的时窗冲突。

各负责人批准；急救与消防随时越过排程。

SC-03

先到对地方，再谈智能

IF-01 / IF-02



提供多语、大字与语音导引，不诊断、不分诊。

医护或服务台决定；固定导视与电话永远可用。

SC-04

AI 帮你说清楚，人来做决定

IF-02 人工服务台



解释公开流程、辅助翻译与表单预检。

工作人员审核；不做资格裁定，不建立个人画像。

测试的不是炫技，是可接管与可退场

低速后勤、合法落点与环境证据把 AI 约束在可复核任务内。

SC-05

配送不抢路，消防不等待

三区后勤线 / TVS



基于已核路线和匿名汇总流量建议错峰。

物业与消防批准；失效时回到人工配送。

SC-06

连接是一个被证明的动作

S2 / 站城到达



比较地图、现场核路与无障碍检查。

缺合法落点即 NO-LINK；删除连接，保留现状路线。

SC-07

不用一块屏幕代表一棵树

环境校准点 / TVS



标注热、风、噪声、空气与雨水数据异常。

专业人员判读；数据差即不可判定，撤设备仍保留低技术改善。


空间在 AI 关闭后仍然成立

包容导行、文化叙事与活动运营都能回到静态、人工和日常状态。

SC-08

不打开手机，也知道公园在哪里

大钟寺到达系统

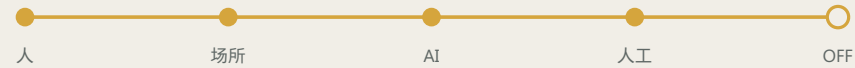

在人工核验路线中给出多语替代路径。

静态地图、触觉地面与站务人员完成基础任务。

SC-09

公园会说话，但不给游客画像

文化节点



从清权史料生成多语、分龄、音频与文字版本。

编辑审核；不追踪游客，版权不清即下架。

SC-10

活动可以关闭，空间继续日常

三区可撤活动节点



比较净宽、疏散、噪声、天气、供电与垃圾冲突。

任一底线失败即取消；撤场后恢复普通使用。

四条日常路径，把场景串成城市生活

科研前场、一日两锚、站城抵达与两翼开放测试，用人物—时间—空间关系验证设计。



七类人物，七个不能被忽略的问题

人物画像不是调研样本统计，而是方案验收的公共利益检查表。

13 / PERSONAS

七种日常，同一条验收顺序

SEVEN EVERYDAY LIVES, ONE SHARED ACCEPTANCE SEQUENCE

人物不是消费者画像；他们用来检验普通服务、人工决策、后勤和无障碍是否被设计保留。

P-01

刘老师

科研运营管理者



NEED

公开而不泄露实验与运维边界

CHECK

关闭前台后，研发与检修仍能正常？

P-02

Maya

来访开发者 / 创业者



NEED

看到来源、日期和人工联系人

CHECK

AI 建议是否会被误读为官方背书？

P-03

王阿姨

社区老人 / 门诊用户



NEED

不用智能手机也能就诊、办事、休息

CHECK

AI 停止时，是否仍有同等人工服务？

P-04

周姐

社区工作者 / 人工治理员



NEED

减少重复解释，保留专业判断

CHECK

她能否立即修改 AI 结果并向居民解释？

P-05

陈同学

通勤学生 / 骑行者



NEED

不参加活动也能最短通过

CHECK

高峰期普通通行能力是否不低于基线？

P-06

李先生

轮椅用户 / 无障碍审阅人



NEED

获得逐段真实可行的路线

CHECK

地图上的连通是否通过了现场核路？

P-07

高师傅

物业 / 设备 / 配送工作者



NEED

全部必要端点可达且可紧急越过排程

CHECK

系统失效时，是否仍能完成检修与清运？

PERSONA ACCEPTANCE FRAME / NOT TO SCALE · NORTH N/A

概念设计可推进 / 工程实施待专业核验

OSM © CONTRIBUTORS, ODbL 1.0 · SNAPSHOT 2026-08-28T14:20:06Z

共同顺序：不打开手机 → 拒绝 AI → 人工决定 → 可申诉 → 可关闭 → 空间仍可用

不是按年份推进，而是按条件解锁

V 并行核验、L 可撤运营、M 概念主方案、D 远期可能性。

14 / PHASING BY TRIGGERS

分期不是时间承诺，而是解锁条件

PHASING IS A SEQUENCE OF PROOF, NOT A CALENDAR PROMISE

L 是 0—1 年运营试点；M 是竞赛主方案；D 只保留为长期可能，不是当前承诺。

V 并行核验 NOW / PARALLEL	L 轻量运营 0-1 YEAR	M 中度复面 1-3 YEAR REFERENCE	D 深度可能 >3 YEAR / NO COMMITMENT
门、时表、消防、停车、后勤、树木、净宽、已批边界	静态导视、纸面时表、人工台、可撤家具、小规模演练	经核首层前沿、院前公共阈、独立后线、地面导视语法	跨楼座联动、站城工程协同；只在全套法定审查后研究
UNLOCK 运营方 + 现场记录	UNLOCK 普通通行/消防/人工等价路径	UNLOCK 产权+结构+消防+排水+停车替代+后勤闭环	UNLOCK 法定审查+资金+运营组织
FALLBACK 修正或删除假设	FALLBACK 任一底线失败即撤场	FALLBACK 任一条件失效退回 L	FALLBACK 无真实公共增量就不进入 D

M_CONCEPT_DESIGN	GO	M_ENGINEERING_IMPLEMENTATION	LOCKED	S2	NO-LINK UNTIL PROVEN
------------------	----	------------------------------	--------	----	----------------------

人负责决定，AI 负责解释与预警


复面运营桌把跨边界冲突放进同一台账，不替代任何法定责任。

15 / OPERATIONS + GOVERNANCE

复面运营桌：让冲突在开启前变得可见

THE RE:FRONT OPERATIONS TABLE MAKES CONFLICTS VISIBLE BEFORE OPENING

这是建议的协作机制，不是已成立机构；各责任主体保留最终判断。

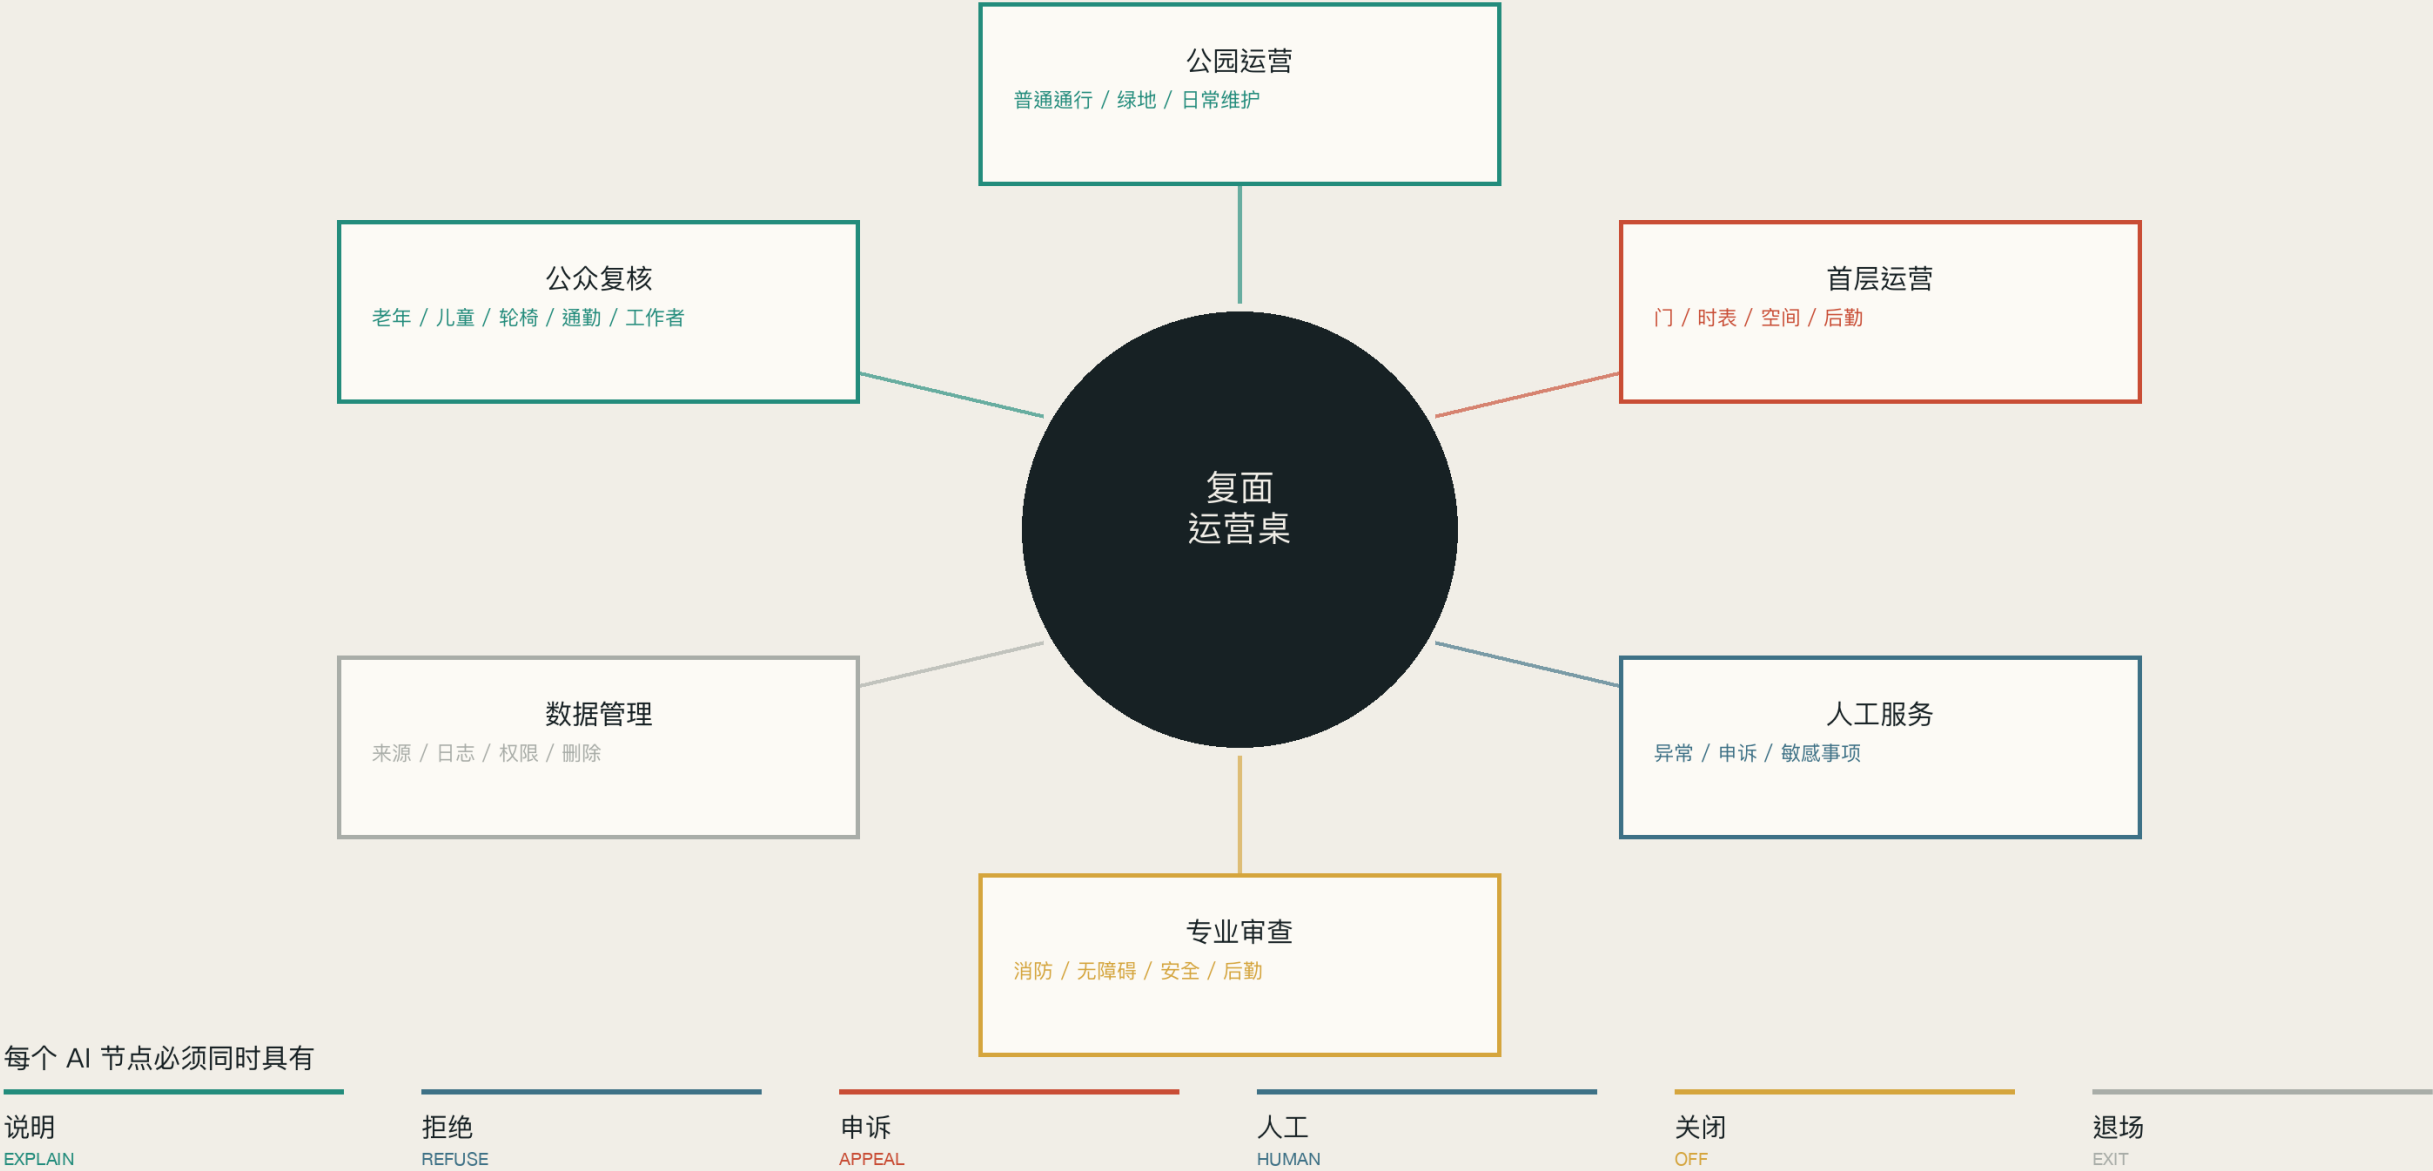

OPERATING MODEL / NOT TO SCALE · NORTH N/A

概念设计可推进 / 工程实施待专业核验

OSM © CONTRIBUTORS, ODbL 1.0 · SNAPSHOT 2026-08-28T14:20:06Z
GREEN 开启 · AMBER 仅人工 · RED 关闭 · EXIT 撤除；AI 不代替法定与专业审查

先守住，再打开

净公共空间、普通通行、生态绩效与后勤连续是增量设计的第一条线。

05 / DESIGN OUTCOMES

从未知基线到可停止的设计成效

FROM UNKNOWN BASELINES TO STOPPABLE OUTCOMES

不把研究计数包装成成效；每项公共回报都从 baseline/TBD、设计底线、核验方法和停止条件开始。

证据覆盖审计 / 非设计绩效		71	29 / 25 / 17	8	1
		A段建筑记录	T1 / T2 / T3 OSM分级	台账待核	局部线索
公共成效	BASELINE	设计底线	核验 / 人工终决	停止条件	
01 净公共空间	TBD / FIELD	Apost ≥ Abase	测绘+运营台账	净面积减少	
02 普通通行	TBD / PEAK	净宽·时长·能力不降	交通/消防/无障碍复核	任一项下降	
03 生态绩效	TBD / SEASONAL	零移树建议；冠幅/渗透/雨洪不退	树木+雨洪基线	移树或能力退化	
04 必要端点可达	TBD / ROUTES	100% VERIFIED	消防/装卸/清运/检修逐点核验	任一端点失达	
05 人工等价服务	TBD / ROSTER	100% AVAILABLE	服务负责人+值守抽查	AI-only 或无人接管	
06 六项治理接口	0 / REGISTER	6 / 6 ACTIVE	说明/拒绝/申诉/人工/关闭/退场	任一缺失	
07 AI-off 演练	0 / DRILL	100% PASS	开放前演练+运行抽查	接管失败	
08 退出与恢复	TBD / OWNER	100% LEDGER	设施/账号/数据/场地责任人签核	无责任人或恢复资源	
09 信息有效性	TBD / VERSION	100% VERIFIED	来源/日期/责任人/过期报警	未核、过期或无来源	
10 公共回报证据	TBD / PURPOSE	1 PUBLIC RECORD / PILOT	目的/结果/失败/纠错/退出公开	只剩宣传或无公共收益	

专业深化触发顺序

- 取得官方边界、法定规划、权属与现状资料。
- 完成结构/机电、消防、医疗、交通/停车、无障碍、生态、排水/市政与运营联合审查。
- 用实测 baseline 复算公共空间、通行、生态与后勤台账。
- 任一专业否定核心假设时，方案降级、修正或删除。

设计承诺

所有动作均为概念建议、参考方案或专业深化触发方案；不声称已取得产权、消防、结构、竣工图、正式红线或实施批准。

OUTCOME LEDGER / BASELINE FLOOR VERIFY STOP

概念设计可推进 / 工程实施待专业核验

OSM © CONTRIBUTORS, ODbL 1.0 · SNAPSHOT 2026-08-28T14:20:06Z

所有 TBD 必须以现场、竣工图或专业台账更新；未建基线不启动工程实施