

30-SECOND P0 IMPLEMENTATION SUMMARY

P0-ALL-STOP-01 · NOT_AUTHORIZED · HOLD

216 m² concept envelope | 3.0 m clear | 12 tasks | 16 BOQ | 8 costs | 6 PASS / 2 HOLD | field 12/12 HOLD | roles unassigned | prices null/TBC


Any group safety-critical failure, missing equivalent, or failed exit => whole unit HOLD

FIXED REVIEW FIGURE 03 / v1.3 P0 FEASIBILITY


P0-ALL-STOP-01 | DIMENSIONED LAUNCH UNIT

NOT_AUTHORIZED · HOLD Unlocated screening concept · no set-out/procurement


1:500 SITE RELATION | CANDIDATE SCREENING ONLY

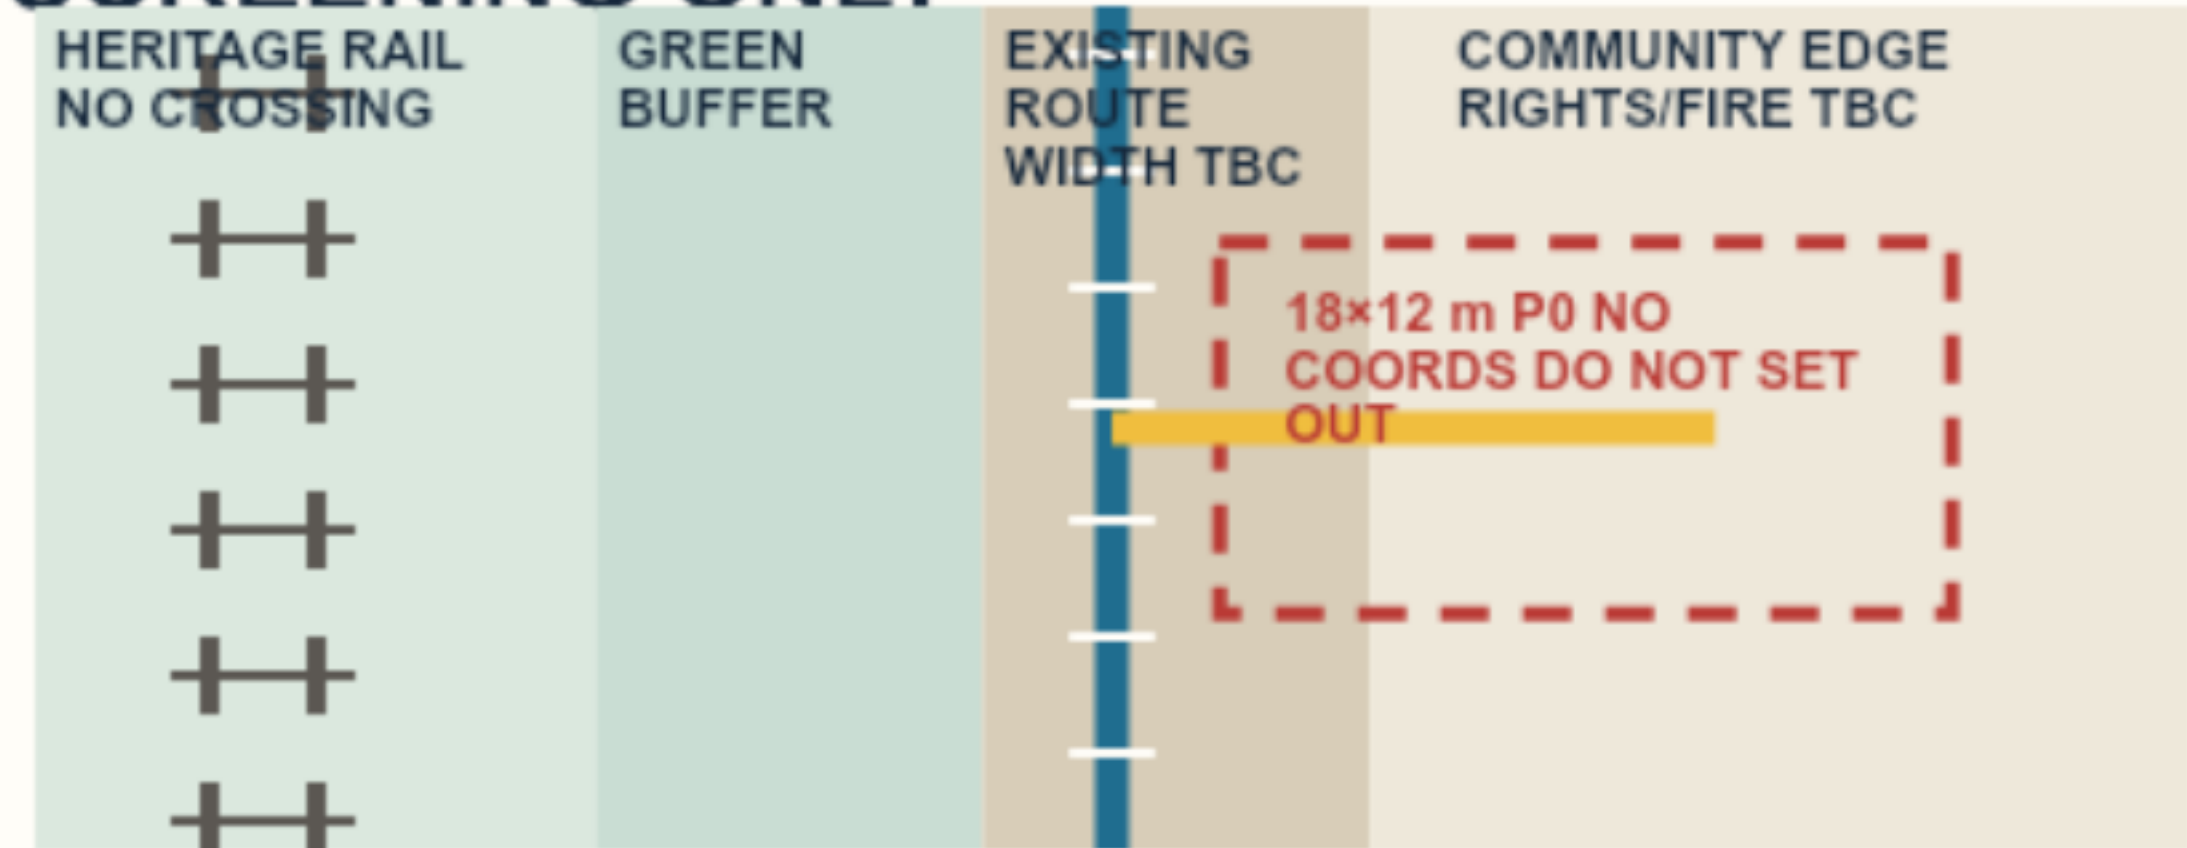


1:50 SECTION | CLEARANCES, INTERFACES, REVERSIBLE COMPONENTS

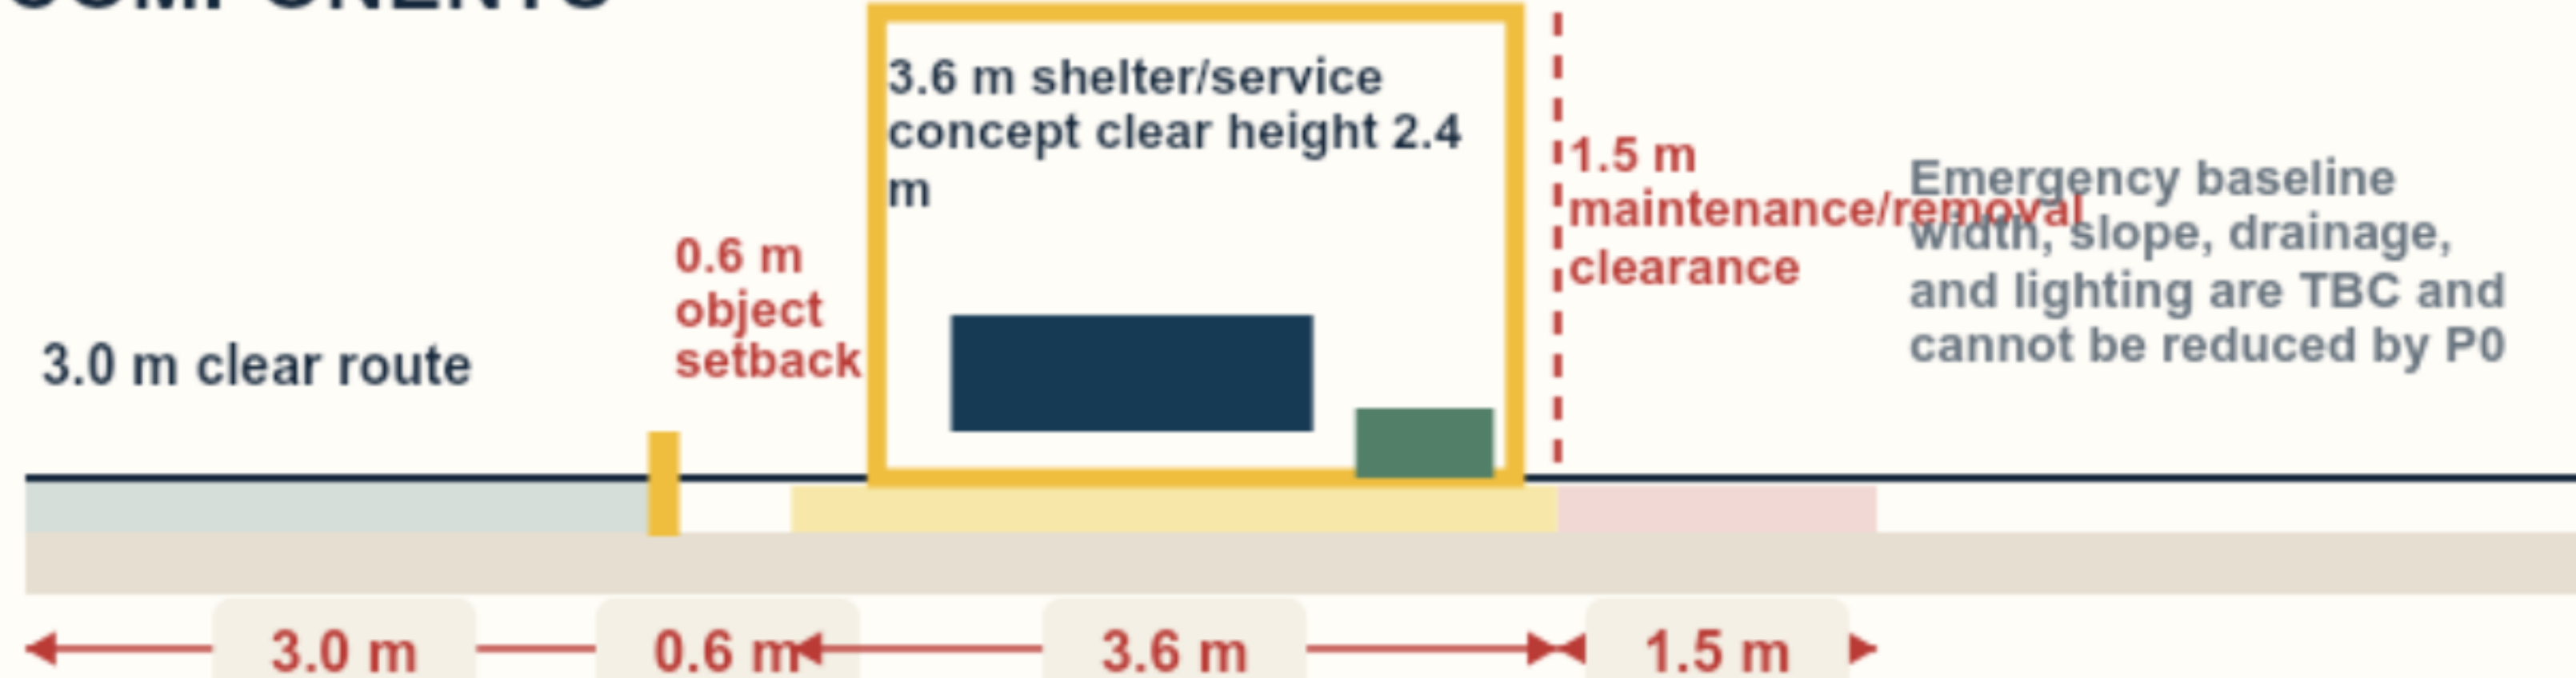

1:100 CONDITIONAL PLAN | ASSUMPTIONS; MOVE / SHRINK / PAUSE / REMOVE

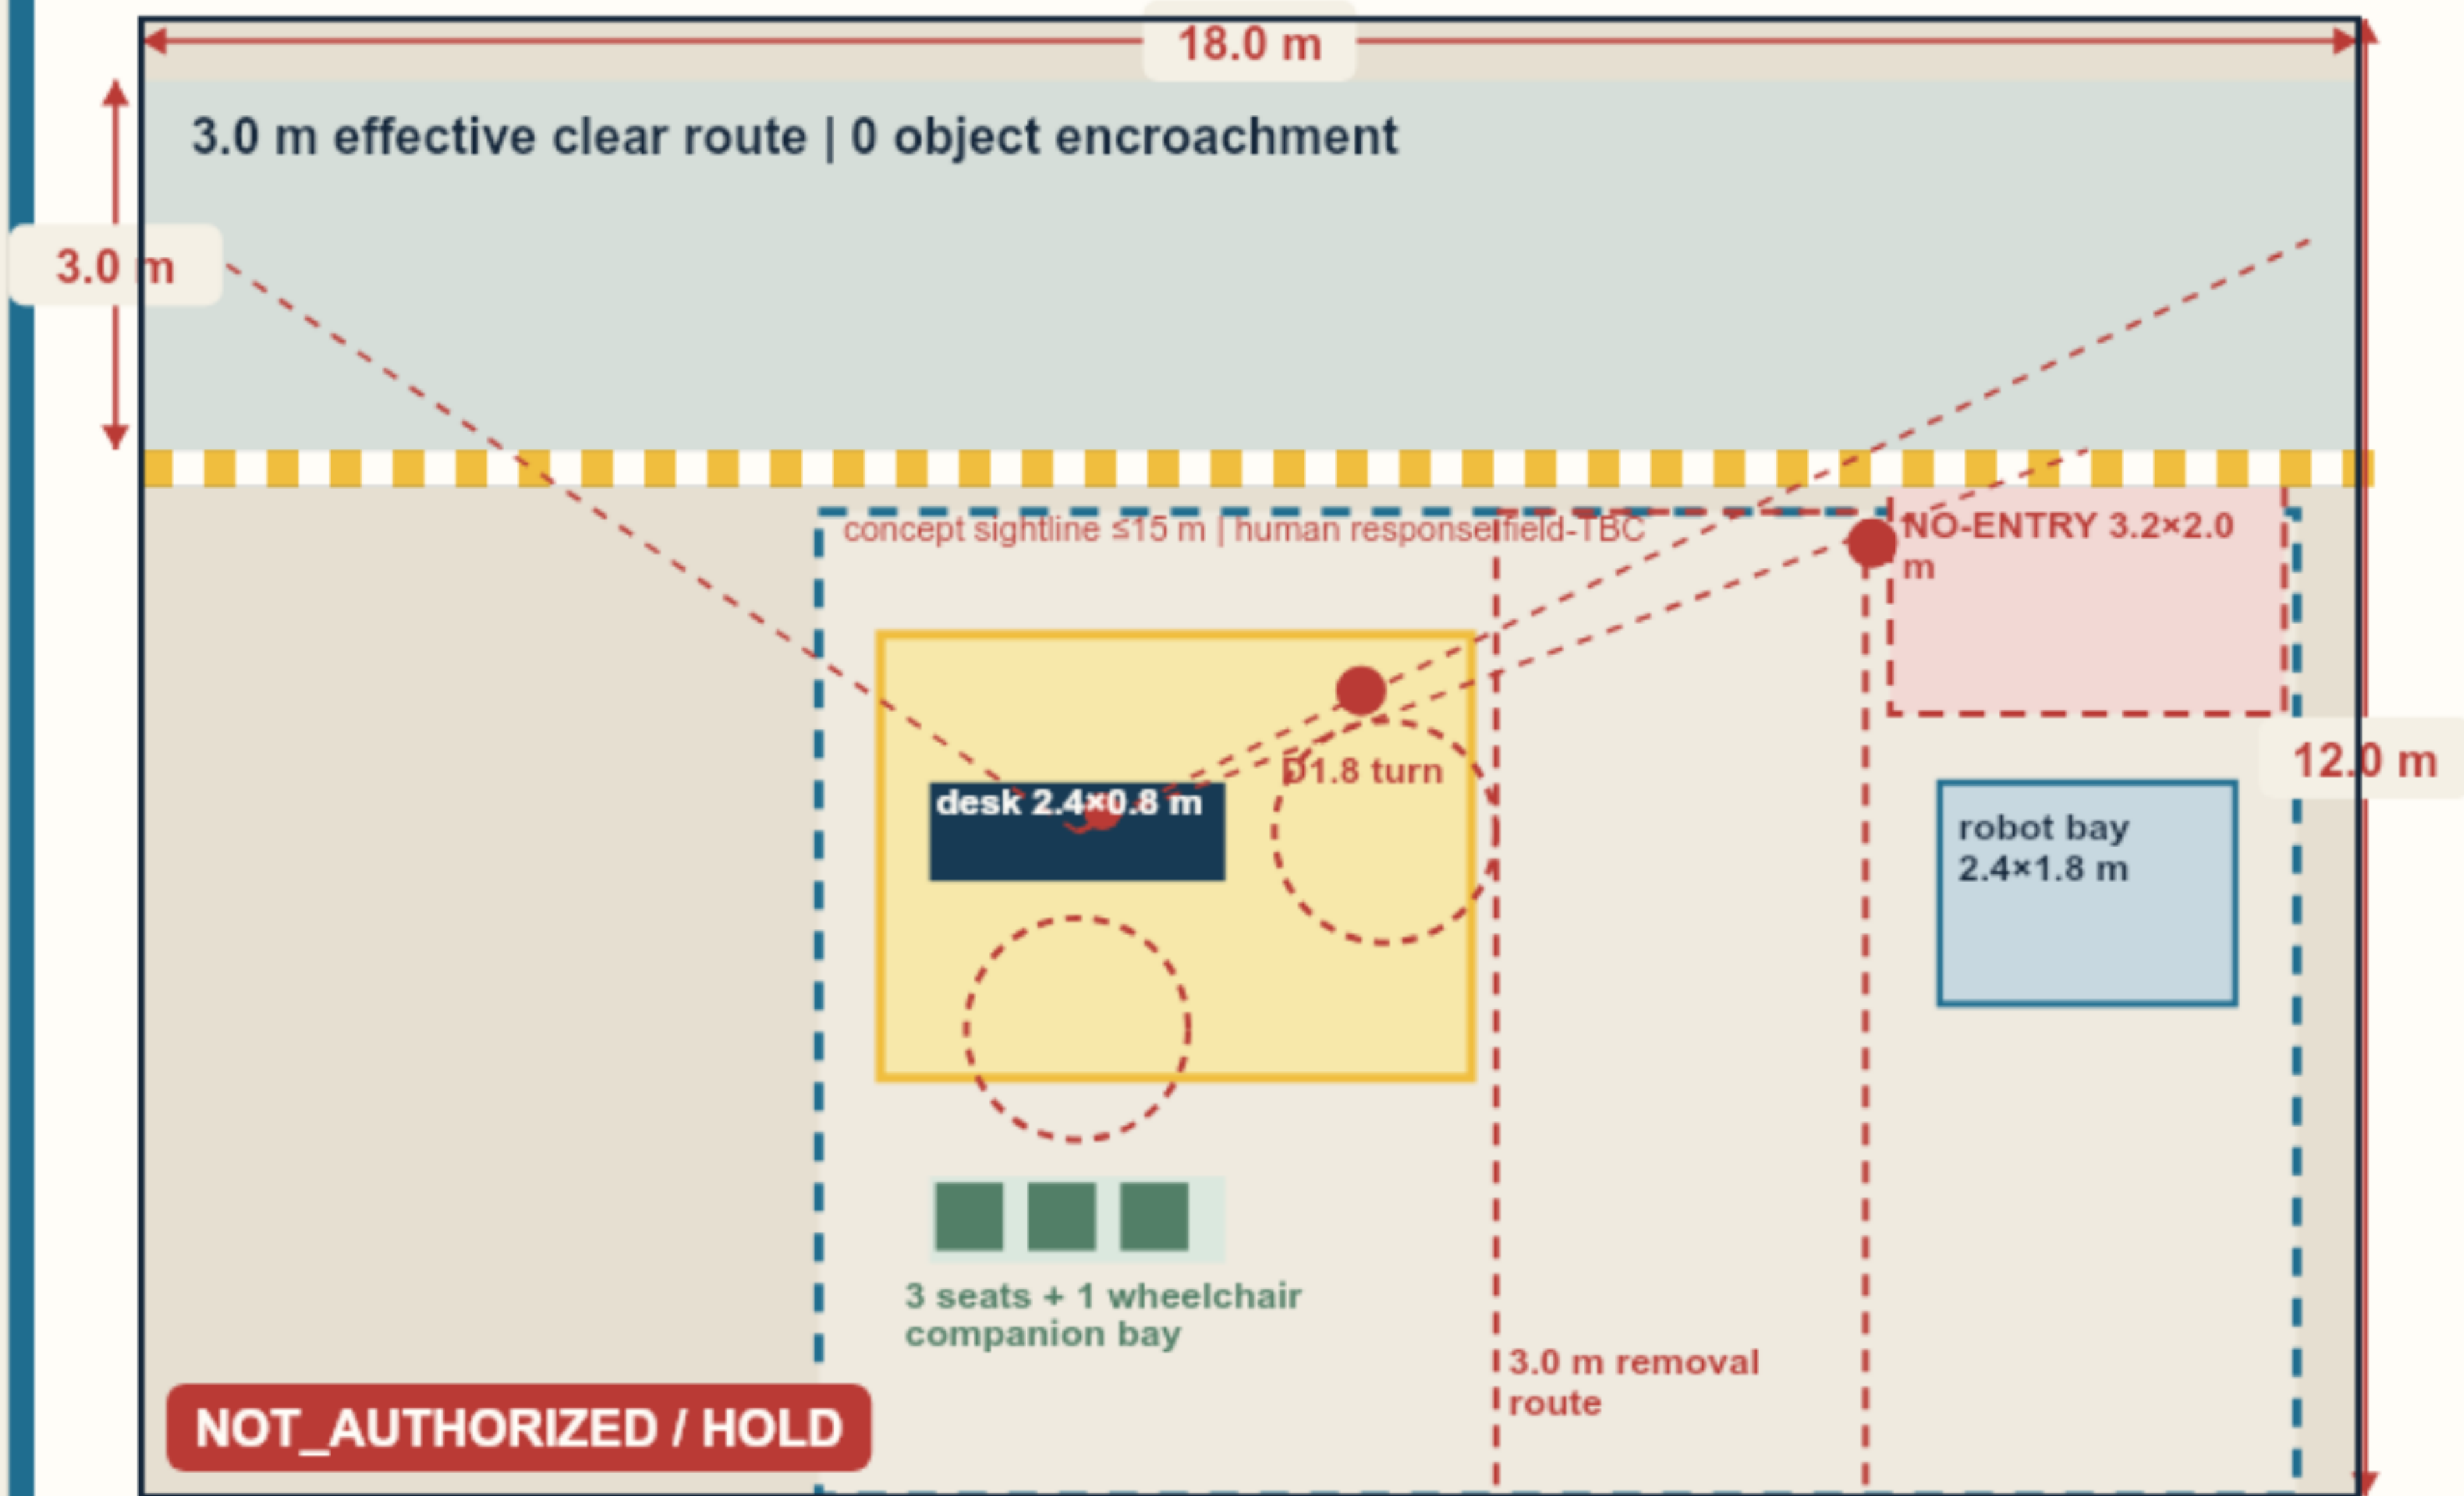

1:20 KEY INTERFACE | REVERSIBLE

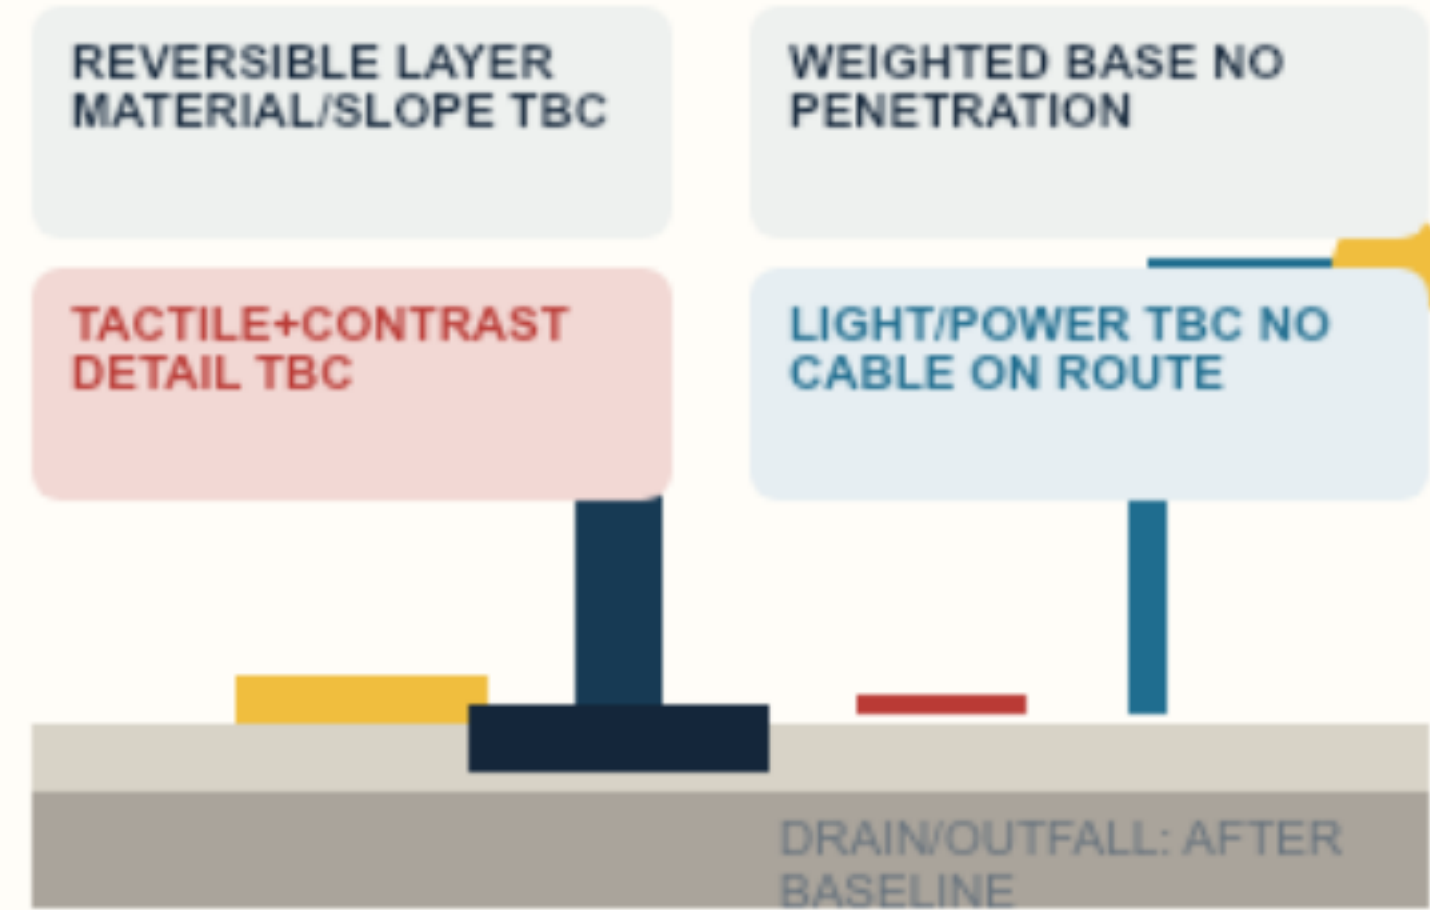

DIMENSIONS | ASSUMPTIONS ONLY

D01	18x12 m	screening envelope
D02	12x8 m	reversible ground
D03	3.0 m	effective clear width
D04	D1.8 m	turning space
D05	2.4 m	desk length
D06	≤15 m	concept sightline
D07	2.4x1.8 m	robot bay
D08	3.2x2.0 m	no-entry zone
D09	0.6 m	object setback
D10	1.5 m	work clearance
D11	3.0 m	removal route
D12	17.28 m²	shelter area

TBC: tactile/contrast, light, drainage, emergency width, capacity

FAILURE CONDITION → AUDITABLE ACTION

MOVE	rights / heritage / fire / utility / drainage conflict	screen-out + new candidate baseline
SHRINK	only if clear route, equivalence, maintenance, exit stay intact	recalculate dimensions / BOQ / roster
PAUSE	roster, audit, weather, light, maintenance, complaint gap	stop log + human takeover + restart decision
REMOVE	critical safety failure, missing equivalence, failed exit, group rejection	incident pack + T12 removal/restoration
RESTORE	day 90 or any removal instruction	before/after + closure + acceptance

FIXED REVIEW FIGURE 05 / v1.3 IMPLEMENTATION EVIDENCE

P0-ALL-STOP-01 · 90 days · G0—G5 fail · stop · exit

P0 TASKS, QUANTITIES, COST + ACCEPTANCE

30 SEC: 216 m² concept envelope | 3.0 m clear | 12 tasks | 16 BOQ lines | 8 costs | roles unassigned | prices null/TBC | NOT_AUTHORIZED + HOLD

90 DAYS → 12 CONTINUOUS TASKS → G0—G5



ACCOUNTABILITY + STOP POWER | ALL unassigned/conditional

execute	R-P0-EXEC
final release/restoration acceptance	A-P0-RIGHTS
immediate stop	co-design / service / safety
human takeover	R-P0-SERVICE
remove/restore	R-P0-INSTALL
independent evidence review	R-P0-EVAL

G0G1G2G3G4G5

6/6 default closed; any user/worker may activate the physical stop without penalty.

NON-PRICED BOQ | 16 PLAN/TASK-DERIVED LINES

P0-Q01	Frame	1 set	P0-Q09	Robot stop line	3.2 m
P0-Q02	Shelter	17.3 m²	P0-Q10	Robot no-entry marking	6.4 m²
P0-Q03	Reversible ground	96 m²	P0-Q11	Seating + companion bay	3+1 bay
P0-Q04	Staffed desk	1 desk	P0-Q12	Lighting points	4 points
P0-Q05	E-stop ×2	2 units	P0-Q13	Interface cabinet + points	1+2 pts
P0-Q06	Paper rack	1 rack	P0-Q14	Install + four checks	1+4 checks
P0-Q07	Wayfinding points	5 points	P0-Q15	Maintenance visits	13 visits
P0-Q08	Tactile / contrast edge	18 m	P0-Q16	Remove + restore	1 lot

Unit rates / formal total / quotation entity / basis date: null / TBC

PARAMETRIC COST | 8 PARTS / 0 RATES

C_P0 = REV + HUMAN + CO-DESIGN + ACCESS/SAFETY + PRIVACY/EVAL + O&M + REMOVE/RESTORE + RESERVE

REV	Reversible space works
HUMAN	Staffed service
CODESIGN	Paid co-design
ACCESS_SAFETY	Accessibility and safety review
PRIVACY_EVAL	Privacy and independent evaluation
OM	Operations and maintenance
REMOVE_RESTORE	Removal and site restoration
RESERVE	Contingency/restoration reserve

Sensitivity: hours, open days, shift overlap, productive FTE hours, co-design support, BOQ quantities, remediation area, contingency.

null / TBC

ACCEPTANCE | A: 6P / 2H | B: 12H

A01	Route connectivity	PASS
A02	Obstacle/encroachment count	PASS
A03	Non-AI equivalent coverage	PASS
A04	Default Gate state	PASS
A05	Audit-record completeness	HOLD
A06	Malformed input triggers HOLD	PASS
A07	Human task remains complete with AI off	HOLD
A08	Exit/restoration process completeness	PASS

B | FIELD BASELINE REQUIRED: wheelchair, low vision, no-smartphone time, human response, conflicts, noise, lighting, drainage, microclimate, residents, roster, actual cost.

Any group safety-critical failure, missing equivalent, or failed exit => whole unit HOLD; no averaging away failure.

SITE GROUNDING / REPRESENTATIVE SEGMENT

VERIFY ORIENTATION, THEN ADD THE DESIGN

Representative segment | orientation + text-only facts + reversible overlay


A ACTUAL ORIENTATION



OSM orientation base. Orange band marks the representative study segment—not a red line or exact site.


B TEXT-ONLY WORKING SKELETON

Published facts translated into a diagram

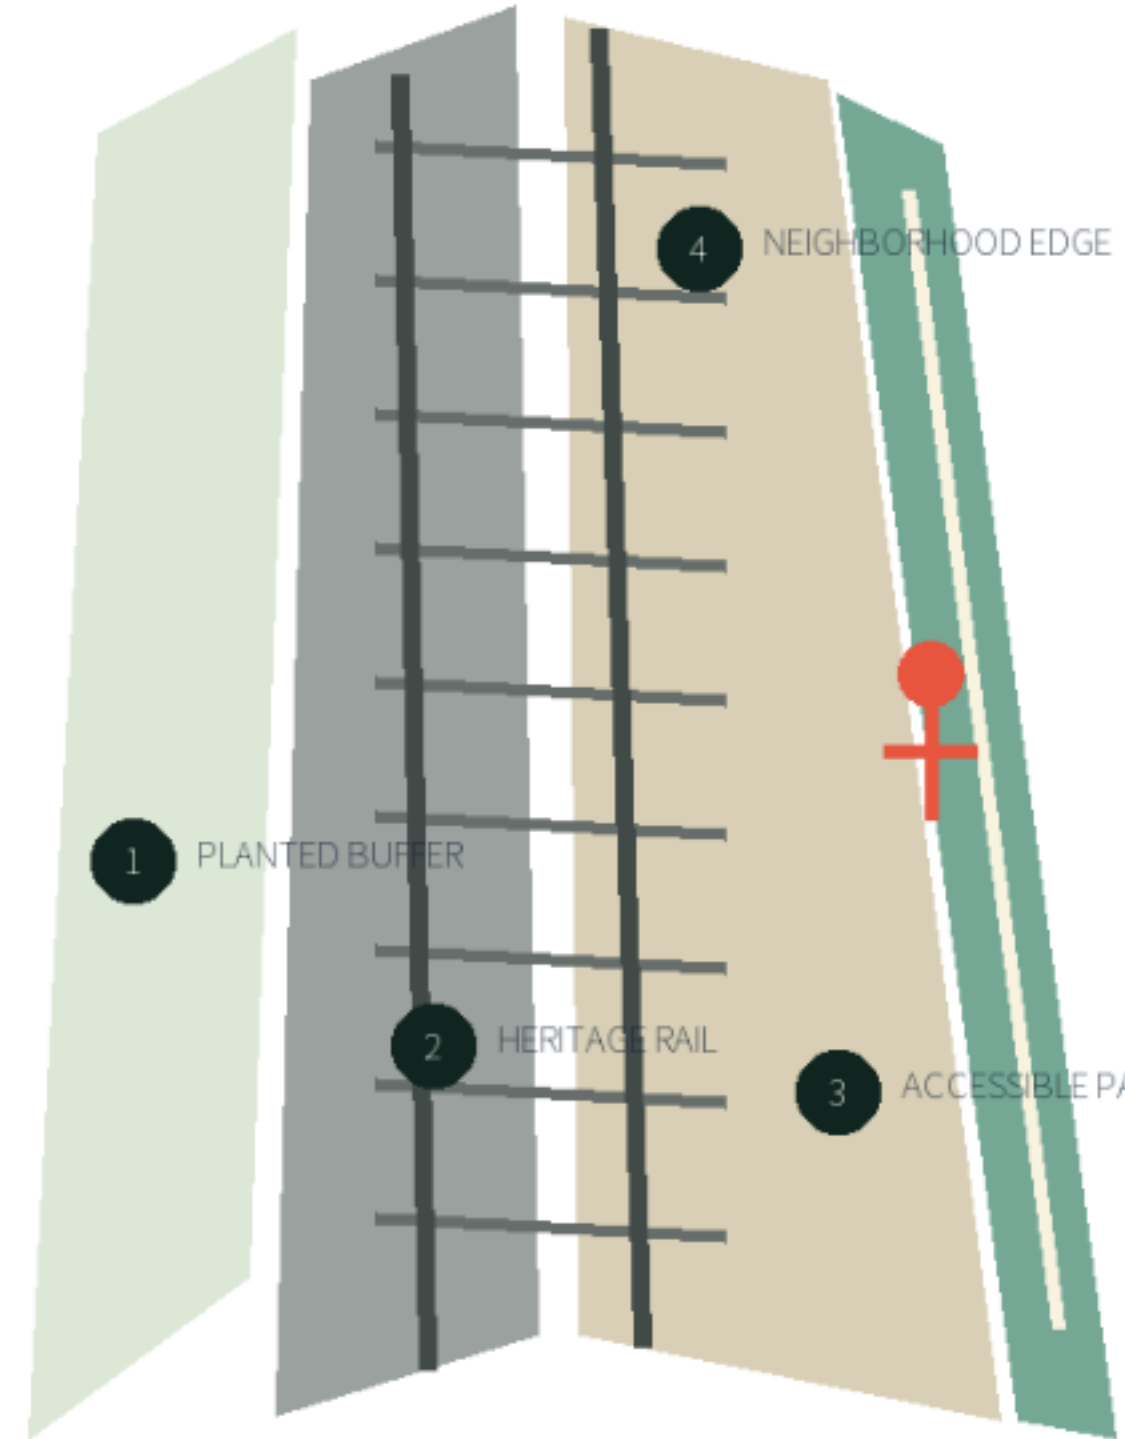

NOT AN EXISTING-CONDITIONS SURVEY. Orientation and published text only.

C REVERSIBLE OVERLAY | NOT APPROVED

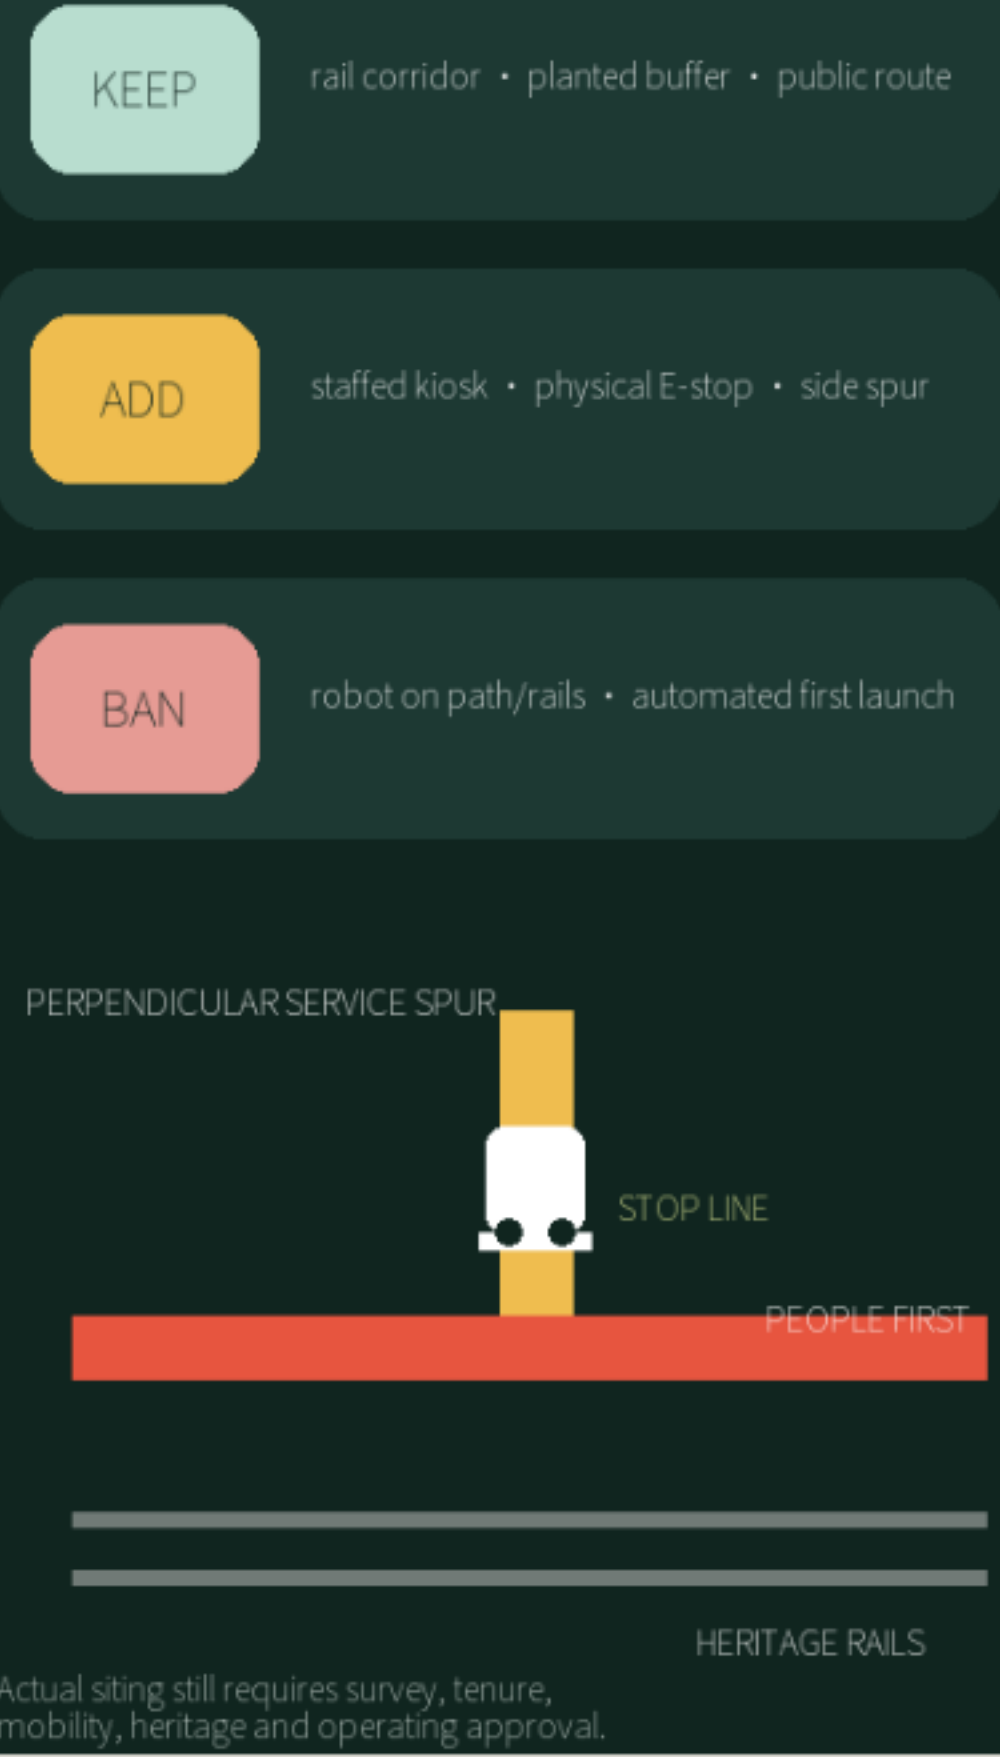

Actual sling still requires survey, tenure, mobility, heritage and operating approval.

Orientation/data: © OpenStreetMap contributors (ODbL), snapshot 2026-08-29. Text facts: Beijing Municipal Government report, 2026-07-30. Not a survey.




THE SLOW LINE | Keep pace with the slowest person

Not slower innovation: a city latency budget for safety, comprehension and choice

01

ONE LINE · THREE YARDS · SIX ALL-STOP GATES

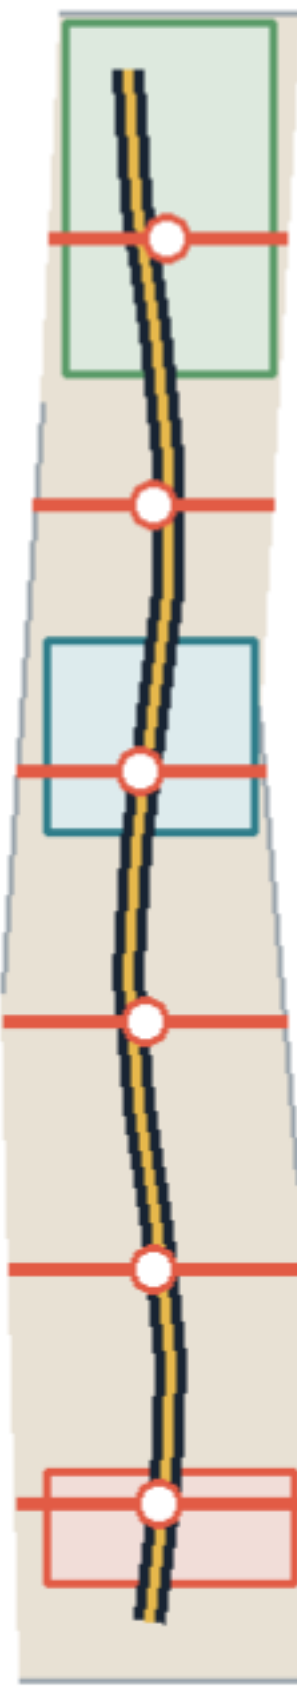

SAFE-SPEED YARD

NO-LOGIN COMMONS

EVERY-STOP MARKET

Dashed = repository provisional envelope; not the real park alignment or planning boundary

SLOWEST-USER TEST · SUT-6

MOBILITY · wheelchairs & slow walkers

SENSORY · low vision & hearing loss

DIGITAL · no phone, no account

LANGUAGE · children & newcomers

CARE · carers & strollers

TIME · night and shift workers

EVERY-STOP CONTRACT

purpose → slowest user → non-AI equivalent → human takeover → minimum data → physical stop → appeal → public review



FROM STRATEGY TO GROUND: THREE LEVELS, ONE DECISION CHAIN 02

43.6 km² research → 11.4 km² provisional container → three transferable prototypes

43.6 km²

RESEARCH: put slowest-first into industry, talent and governance

11.4 km²

OVERALL DESIGN: one Slow Line and six all-stop gates

3 AREAS

KEY DESIGN: Safe-Speed, No-Login, Every-Stop

CONCEPT LAND USE | RECOMPUTABLE



LEGEND

- R&D
- Housing
- Service
- Commerce
- Culture
- Education
- Green
- Plaza

Concept only · replace when official controls arrive

ONE MAP: SPACE × SERVICE × OPERATIONS

SPACE

- continuous accessible line
- six cross-city gates
- three reversible yards

SERVICE

- works without login
- a human is findable
- non-AI path is equivalent

OPERATE

- pilot before building
- failure defaults to stop
- publish review before scale


Official geometry → replace constraints → regenerate all layers, metrics, figures and PDFs



MOBILITY + BLUE-GREEN: THE FASTEST SYSTEM MUST WAIT 04

continuity, crossings, rest, help and stop authority before spectacle

CONCEPT NETWORK — NOT ROAD OR PARK ALIGNMENT

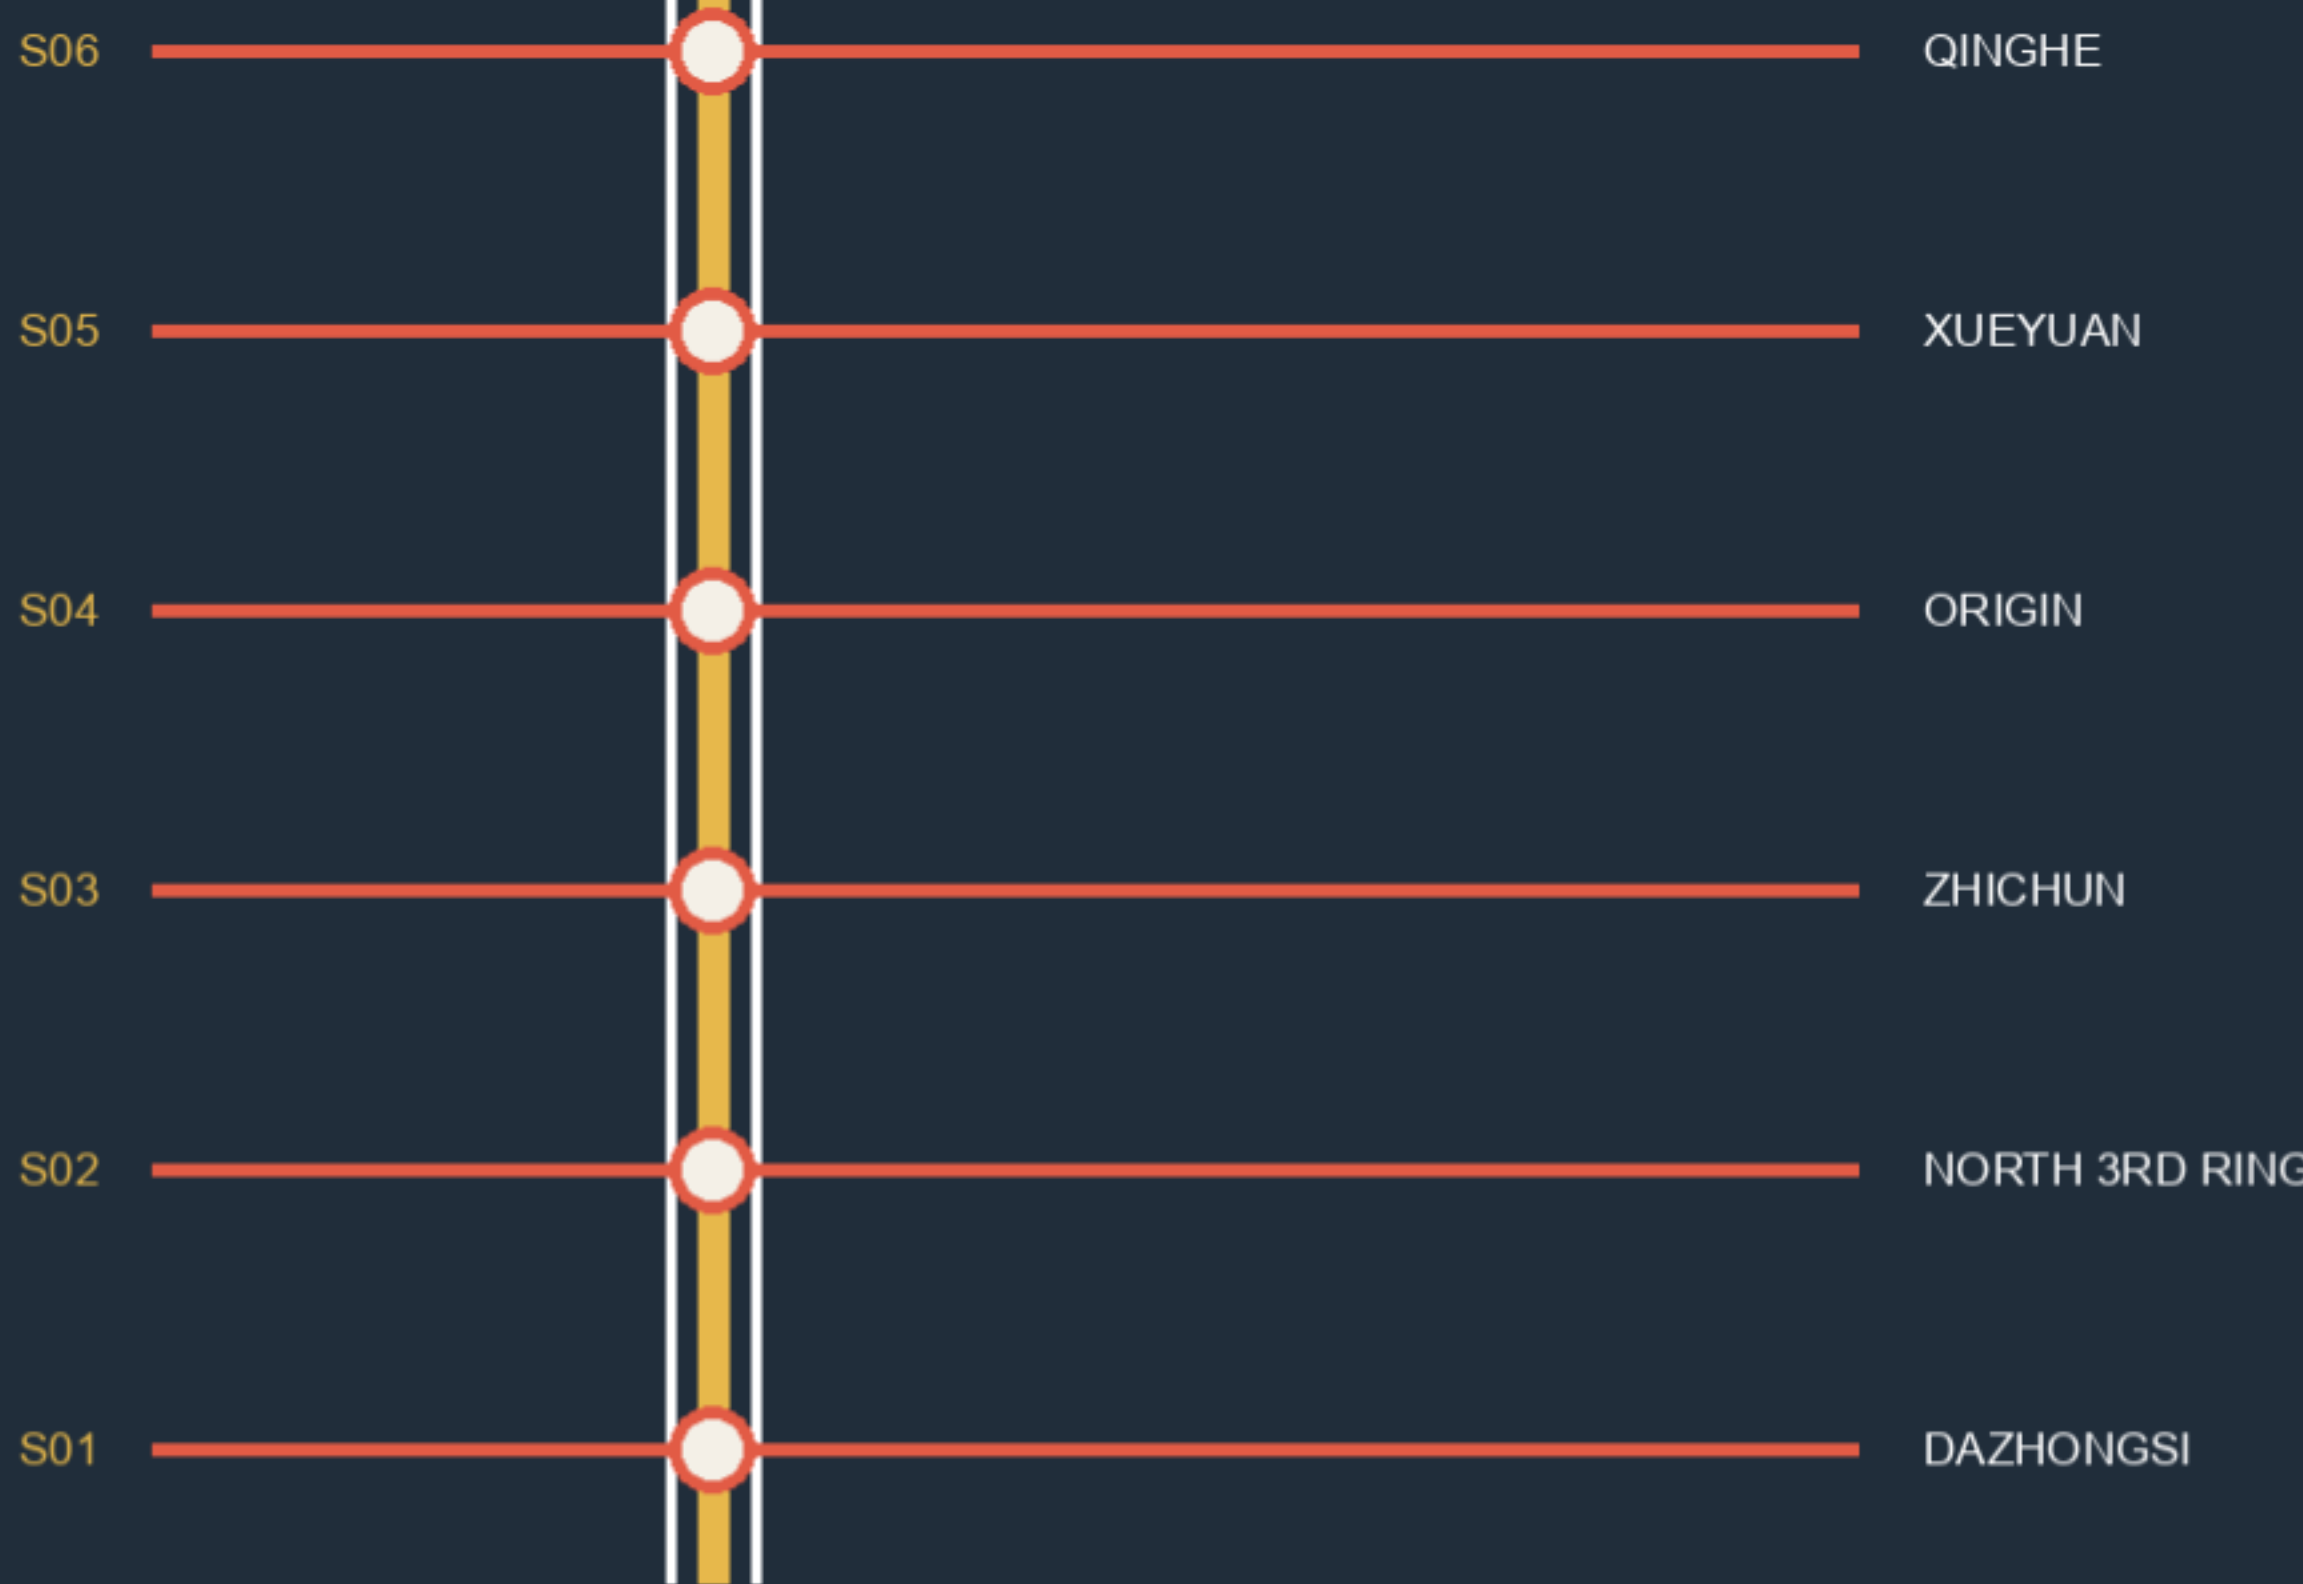

FIVE PERFORMANCE GATES

01 STEP-FREE CONTINUITY

detours do not count as access

02 REST + SHADE

spacing tested by slowest users

03 MULTI-SENSORY

visual, audio and tactile

04 HUMAN IS FINDABLE

on-site, phone and paper

05 ROBOTS CAN STOP

physical stop beats inference

NO SITE BASELINE: thresholds require co-design and professional review